2014169381
RECORDED IN
PUBLIC RECORDS PINELLAS COUNTY
FL
BK: 139 PG:43-45
06/13/2014 at 04:41 PM
KEN BURKE, CLERK OF COURT AND COMPTROLLER

SUBDIVISION PLAT

PLAT BOOK: 139 PAGE: 43

COVE AT INDIAN ROCKS BEACH

PLAT BOOK _____ PAGE _____

PORTION OF SECTION 12, TOWNSHIP 30 SOUTH, RANGE 14 EAST,
CITY OF INDIAN ROCKS BEACH, PINELLAS COUNTY, FLORIDA

AND A REPLAT OF LOTS 3, 4, 5, 6, 7, 9, 10, AND A PORTION OF LOTS 8 AND 14, BLOCK 5 AND LOTS 9, 10, 11, 12 AND 13, BLOCK 4 AND A PORTION OF VACATED CANAL AVENUE NORTH AND A PORTION OF VACATED 1ST STREET OF HAVEN BEACH, ACCORDING TO THE MAP OR PLAT THEREOF AS RECORDED IN PLAT BOOK 5, PAGE 27, OF THE PUBLIC RECORDS OF PINELLAS COUNTY, FLORIDA AND LOT 1, HOLIDAY RECREATIONAL VEHICLE RESORT, ACCORDING TO THE MAP OR PLAT THEREOF AS RECORDED IN PLAT BOOK 111, PAGES 1 AND 2, OF THE PUBLIC RECORDS OF PINELLAS COUNTY, FLORIDA

DESCRIPTION

A PARCEL OF LAND LYING IN A PORTION OF SECTION 12, TOWNSHIP 30 SOUTH, RANGE 14 EAST, AND LOTS 3, 4, 5, 6, 7, 9, 10, AND A PORTION OF LOTS 8 AND 14, BLOCK 5 AND LOTS 9, 10, 11, 12 AND 13, BLOCK 4 AND A PORTION OF VACATED CANAL AVENUE NORTH AND A PORTION OF VACATED 1ST STREET OF HAVEN BEACH, ACCORDING TO THE MAP OR PLAT THEREOF AS RECORDED IN PLAT BOOK 5, PAGE 27, OF THE PUBLIC RECORDS OF PINELLAS COUNTY, FLORIDA AND LOT 1, HOLIDAY RECREATIONAL VEHICLE RESORT, ACCORDING TO THE MAP OR PLAT THEREOF AS RECORDED IN PLAT BOOK 111, PAGES 1 AND 2, OF THE PUBLIC RECORDS OF PINELLAS COUNTY, FLORIDA BEING MORE PARTICULARLY DESCRIBED AS FOLLOWS:

AS A POINT OF REFERENCE COMMENCE AT THE NORTHWEST CORNER OF LOT 1, BLOCK 5 OF SAID HAVEN BEACH AND PROCEED S 05°58'12" E, ALONG THE WEST BOUNDARY OF LOTS 1 AND 2 OF SAID PLAT OF HAVEN BEACH, A DISTANCE OF 100.32 FEET TO THE POINT OF BEGINNING; THENCE S 89°26'28" E, ALONG THE SOUTH BOUNDARY OF SAID LOT 2, A DISTANCE OF 101.61 FEET TO THE NORTHWEST CORNER OF LOT 19, BLOCK 5 OF SAID HAVEN BEACH; THENCE S 06°47'56" E, ALONG THE WEST BOUNDARY OF SAID LOT 19, A DISTANCE OF 50.13 FEET TO THE NORTHWEST CORNER OF LOT 18, BLOCK 5 OF SAID HAVEN BEACH; THENCE S 02°57'59" E, ALONG THE WEST BOUNDARY OF LOTS 18 AND 17, BLOCK 5 OF SAID HAVEN BEACH, A DISTANCE OF 100.23 FEET TO THE NORTHWEST CORNER OF LOT 16, BLOCK 5 OF SAID HAVEN BEACH; THENCE S 02°50'26" E, ALONG THE WEST BOUNDARY OF SAID LOT 16, A DISTANCE OF 50.06 FEET; THENCE S 00°07'38" W, ALONG THE WEST BOUNDARY OF LOTS 16 AND 15, A DISTANCE OF 58.27 FEET TO THE NORTHWEST CORNER OF LOT 14, BLOCK 5 OF SAID HAVEN BEACH; THENCE S 01°07'41" W TO A POINT ON THE SOUTH BOUNDARY OF THE NORTH HALF (1/2), A DISTANCE OF 18.93 FEET; THENCE S 89°07'49" E, ALONG SAID SOUTH BOUNDARY, A DISTANCE OF 24.57 FEET; THENCE S 01°01'49" E, A DISTANCE OF 20.48 FEET TO THE NORTHEAST CORNER OF LOT 11, BLOCK 5 OF SAID HAVEN BEACH; THENCE N 88°03'06" W, ALONG THE NORTH BOUNDARY OF SAID LOT 11, A DISTANCE OF 50.19 FEET TO THE NORTHWEST CORNER OF SAID LOT 11; THENCE S 00°54'26" W, ALONG THE WEST BOUNDARY OF SAID LOT 11 AND A SOUTHERLY PROJECTION THEREOF, A DISTANCE OF 113.47 FEET TO A POINT ON THE MEAN HIGH WATER LINE AS ESTABLISHED BY A SURVEY DATED OCTOBER 11, 2006; THENCE ALONG SAID MEAN HIGH WATER LINE THE FOLLOWING SIXTEEN (16) COURSES, (1) S 79°45'27"W, A DISTANCE OF 13.17 FEET; THENCE (2) N 89°49'10"W, A DISTANCE OF 49.89 FEET; THENCE (3) S 88°53'50" W, A DISTANCE OF 39.93 FEET; THENCE (4) S 85°58'36" W, A DISTANCE OF 34.53 FEET; THENCE (5) N 89°37'51" W, A DISTANCE OF 52.08 FEET; THENCE (6) N 00°04'49" E, A DISTANCE OF 5.60 FEET; THENCE (7) S 85°16'51" W, A DISTANCE OF 52.46 FEET; THENCE (8) S 89°29'58" W, A DISTANCE OF 27.19 FEET; THENCE (9) S 83°47'20" W, A DISTANCE OF 6.27 FEET; THENCE (10) N 89°31'44"W, A DISTANCE OF 7.48 FEET; THENCE (11) N 71°35'18" W, A DISTANCE OF 13.44 FEET; THENCE (12) N 80°47'00"W, A DISTANCE OF 32.61 FEET; THENCE (13) N 70°38'55" W, A DISTANCE OF 46.32 FEET; THENCE (14) N 40°35'43" W, A DISTANCE OF 52.60 FEET; THENCE (15) N 13°32'22" W, A DISTANCE OF 38.42 FEET; THENCE (16) N 07°08'39" E, A DISTANCE OF 31.78' TO A POINT ON THE SOUTH BOUNDARY OF LOT 8, BLOCK 4 OF SAID HAVEN BEACH; THENCE S 87°25'45" E, ALONG THE SOUTH BOUNDARY OF SAID LOT 8, A DISTANCE OF 147.78 FEET TO THE SOUTHEAST CORNER OF SAID LOT 8; THENCE N 16°32'57" E, ALONG THE EAST BOUNDARY OF SAID LOT 8 AND THE EAST BOUNDARY OF TECZA'S CASA CONDOMINIUM PLAT BOOK 132, PAGES 6–8, OF THE PUBLIC RECORDS OF PINELLAS COUNTY, FLORIDA AND LYON'S DEN CONDOMINIUM PLAT BOOK 130, PAGES 50–52 OF THE PUBLIC RECORDS OF PINELLAS COUNTY, FLORIDA, A DISTANCE OF 169.45 FEET TO THE NORTHEAST CORNER OF SAID LYON'S DEN CONDOMINIUM; THENCE N 88°00'51"W, ALONG THE NORTH BOUNDARY OF SAID LYON'S DEN CONDOMINIUM, A DISTANCE OF 152.90 FEET TO A POINT ON THE AFOREMENTIONED MEAN HIGH WATER LINE; THENCE ALONG SAID MEAN HIGH WATER LINE THE FOLLOWING EIGHT (8) COURSES, (1) N 05°58'10" W, A DISTANCE OF 14.35 FEET; THENCE (2) N 25°48'14" W, A DISTANCE OF 30.60 FEET; THENCE (3) N 51°30'39" W, A DISTANCE OF 32.73 FEET; THENCE (4) N 58°43'36" W, A DISTANCE OF 41.75 FEET; THENCE (5) S 79°39'01" W, A DISTANCE OF 1.04 FEET; THENCE (6) S 70°02'58" W, A DISTANCE OF 8.33 FEET; THENCE (7) S 26°46'54" W, A DISTANCE OF 9.92 FEET; THENCE (8) N 87°24'46" W, A DISTANCE OF 7.39 FEET TO A POINT ON THE EAST RIGHT–OF–WAY LINE OF GULF BOULEVARD (COUNTY ROAD 699) SAID POINT BEING ON A CURVE CONCAVE EASTERLY HAVING A RADIUS OF 924.93 FEET AND A CHORD BEARING AND DISTANCE OF N 08°04'20" E, 173.85 FEET; THENCE ALONG THE ARC OF SAID CURVE TO THE RIGHT, 174.11 FEET TO A POINT ON THE SOUTH RIGHT–OF–WAY LINE OF 7TH AVENUE NORTH; THENCE S 89°27'18" E, ALONG SAID SOUTHERLY RIGHT–OF–WAY LINE, A DISTANCE OF 312.56 FEET TO A POINT ON THE WEST RIGHT–OF–WAY LINE OF 1ST STREET; THENCE S 05°50'19" E, ALONG SAID WEST RIGHT–OF–WAY LINE, A DISTANCE OF 100.31 FEET; THENCE S 89°26'28"E, A DISTANCE OF 40.27 FEET TO THE POINT OF BEGINNING. PARCEL CONTAINING 4.19 ACRES MORE OR LESS.

CERTIFICATE OF OWNERSHIP AND DEDICATION

THE UNDERSIGNED, TAYLOR MORRISON OF FLORIDA, INC., A FLORIDA CORPORATION, CERTIFIES OWNERSHIP OF THE PROPERTY DESCRIBED HEREIN AND HAS CAUSED THIS PLAT ENTITLED "COVE AT INDIAN ROCKS BEACH" TO BE MADE AND SUBJECT TO THE TERMS OF THE DECLARATION OF PROTECTIVE COVENANTS, RESTRICTIONS AND EASEMENTS TO BE RECORDED SIMULTANEOUSLY WITH THIS PLAT, DOES HEREBY DEDICATE THE FOLLOWING TO THE CITY OF INDIAN ROCKS BEACH:

A) A NON–EXCLUSIVE INGRESS & EGRESS EASEMENT ACROSS THE PRIVATE ROAD RIGHT–OF–WAY (TRACT A) FOR EMERGENCY AND LAW ENFORCEMENT PERSONNEL SERVING THE SUBDIVISION; AND
B) A NON–EXCLUSIVE PEDESTRIAN AND GOLF CART EASEMENT ACROSS A PORTION OF TRACT C IDENTIFIED AS "EASEMENT F–PUBLIC EASEMENT" TOGETHER WITH THE RIGHT TO CONSTRUCT, MAINTAIN, REPAIR OR INSTALL SIDEWALKS OR LANDSCAPE MATERIALS LOCATED THEREIN.

RESERVATIONS

THE DEVELOPER RESERVES THE RIGHT TO TRANSFER ALL OTHER EASEMENTS SHOWN ON THE PLAT TO PRIVATE UTILITY PROVIDERS, PINELLAS COUNTY, COVE AT INDIAN ROCKS BEACH HOMEOWNERS ASSOCIATION, INC., AND TO INDIVIDUAL LOT OWNERS AS FURTHER DEFINED IN THE DECLARATION OF PROTECTIVE COVENANTS, RESTRICTIONS AND EASEMENTS FOR COVE AT INDIAN ROCKS BEACH TO BE RECORDED SIMULTANEOUSLY WITH THIS PLAT.

THE DEVELOPER RESERVES THE RIGHT TO TRANSFER EASEMENTS OVER TRACT A FOR ACCESS AND UTILITIES, TRACT B FOR USE AND EASEMENT G FOR A SEWER LINE TO NEIGHBORING PROPERTY OWNERS.

IN WITNESS WHEREOF, I HAVE HEREUNTO SET MY HAND THIS 4th DAY OF June, 2014.

TAYLOR MORRISON OF FLORIDA, INC., A FLORIDA CORPORATION

BY: _____
ANTHONY SQUITIERI, VICE PRESIDENT
STATE OF FLORIDA
COUNTY OF SARASOTA

WITNESS: Becky Ellington
PRINT NAME: Becky Ellington

WITNESS: _____
PRINT NAME: David Truxton

THE FOREGOING INSTRUMENT WAS ACKNOWLEDGED BEFORE ME THIS 4th DAY OF JUNE 2014, BY ANTHONY SQUITIERI, AS VICE PRESIDENT OF TAYLOR MORRISON OF FLORIDA, INC., A FLORIDA CORPORATION, ON BEHALF OF THE CORPORATION, WHO IS PERSONALLY KNOWN TO ME OR PRODUCED_____ AS IDENTIFICATION.

NOTARY PUBLIC SIGNATURE: Deborah K. Beckett
PRINT NAME: DEBORAH K. BECKETT
COMMISSION NO: EE 121571
MY COMMISSION EXPIRES: Aug 14, 2015

DEBORAH K BECKETT
MY COMMISSION #EE121571
EXPIRES: AUG 14, 2015
Bonded through Huntleberry Notary Bonding, Inc.

PREPARED BY:

HAMILTON
ENGINEERING & SURVEYING, INC.

311 NORTH NEWPORT AVENUE
TAMPA, FL 33606 CERTIFICATE OF AUTHORIZATION LB#7013
TEL (813) 250-3535
FAX (813) 250-3636

CERTIFICATE OF APPROVAL OF COUNTY CLERK:

STATE OF FLORIDA } SS
COUNTY OF PINELLAS

I, KEN BURKE, CLERK OF THE CIRCUIT COURT OF PINELLAS COUNTY, FLORIDA HEREBY CERTIFY THAT THIS PLAT HAS BEEN EXAMINED AND THAT IT COMPLIES IN FORM WITH ALL THE REQUIREMENTS OF THE STATUTES OF THE STATE OF FLORIDA PERTAINING TO MAPS AND PLATS, AND THAT THIS PLAT HAS BEEN FILED FOR RECORD IN PLAT BOOK 139, PAGES 43-45 OF THE PUBLIC RECORDS OF PINELLAS COUNTY, FLORIDA THIS 13TH DAY OF JUNE, 2014 @ 4:41 PM

KEN BURKE, CLERK
PINELLAS COUNTY, FLORIDA

BY: _____
DEPUTY CLERK
PETAR VLACIC
PRINT

PINELLAS COUNTY, FLORIDA CIRCUIT COURT

CERTIFICATE OF APPROVAL OF CITY OF INDIAN ROCKS BEACH COMMISSION:

STATE OF FLORIDA } SS
COUNTY OF PINELLAS

IT IS HEREBY CERTIFIED THAT THIS PLAT HAS BEEN OFFICIALLY APPROVED FOR RECORD AND ALL OFFERS OF DEDICATION ACCEPTED BY THE CITY OF INDIAN ROCKS BEACH, PINELLAS COUNTY, FLORIDA, THIS 6th DAY OF June, 2014.

R. B. JOHNSON, MAYOR

Deanne B. O'Reilly
CLERKS CERTIFICATION AND APPROVAL
BY: DEANNE BULINO O'REILLY, CITY CLERK

REVIEWED FOR CONFORMITY:

The undersigned as representative of CivilSurv Design Group, Inc., under contract to the City of Indian Rocks Beach, Pinellas County, Florida, has reviewed this plat for conformity to Chapter 177, Part 1, Florida Statutes, relating to the making of maps and plats.

Gary L. Allen, P.L.S.
Florida Registration No. 4756
CivilSurv Design Group, Inc.
Florida Registration No. LB 7805

6-5-14
Date:

GARY L. ALLEN CERTIFICATE No. 4756 STATE OF FLORIDA

SURVEYOR'S CERTIFICATE

I, RICHARD C. HINSON, THE UNDERSIGNED PROFESSIONAL SURVEYOR AND MAPPER, HEREBY CERTIFY THAT THIS PLAT OF "COVE AT INDIAN ROCKS BEACH" IS A TRUE AND CORRECT REPRESENTATION OF THE LANDS SURVEYED, AND THAT THE SURVEY WAS MADE UNDER MY RESPONSIBLE DIRECTION AND SUPERVISION. I FURTHER CERTIFY THAT THIS PLAT COMPLIES WITH SECTION 177.091 OF CHAPTER 177 OF THE LAWS OF THE STATE OF FLORIDA PERTAINING TO MATERIALS AND COMPOSITION AND THAT THE PERMANENT REFERENCE MONUMENTS WERE SET AS INDICATED AS OF NOVEMBER 12, 2013 AND LOT CORNERS WILL BE SET IN ACCORDANCE WITH THE REQUIREMENTS OF CHAPTER 177, FLORIDA STATUTES.

Richard C. Hinson, PSM
FLORIDA PROFESSIONAL SURVEYOR AND MAPPER #LS3840
HAMILTON ENGINEERING AND SURVEYING, INC.
CERTIFICATE OF AUTHORIZATION LB #7013
311 NORTH NEWPORT AVENUE
TAMPA, FLORIDA 33606

6/3/14
Date

RICHARD C. HINSON LICENSE No. 3840 STATE OF FLORIDA

COVE AT INDIAN ROCKS BEACH

PLAT BOOK _____ PAGE _____

PORTION OF SECTION 12, TOWNSHIP 30 SOUTH, RANGE 14 EAST,
CITY OF INDIAN ROCKS BEACH, PINELLAS COUNTY, FLORIDA

AND A REPLAT OF LOTS 3, 4, 5, 6, 7, 9, 10, AND A PORTION OF LOTS 8 AND 14, BLOCK 5 AND LOTS 9, 10, 11, 12 AND 13, BLOCK 4 AND A PORTION OF VACATED CANAL AVENUE NORTH AND A PORTION OF VACATED 1ST STREET OF HAVEN BEACH, ACCORDING TO THE MAP OR PLAT THEREOF AS RECORDED IN PLAT BOOK 5, PAGE 27, OF THE PUBLIC RECORDS OF PINELLAS COUNTY, FLORIDA AND LOT 1, HOLIDAY RECREATIONAL VEHICLE RESORT, ACCORDING TO THE MAP OR PLAT THEREOF AS RECORDED IN PLAT BOOK 111, PAGES 1 AND 2, OF THE PUBLIC RECORDS OF PINELLAS COUNTY, FLORIDA

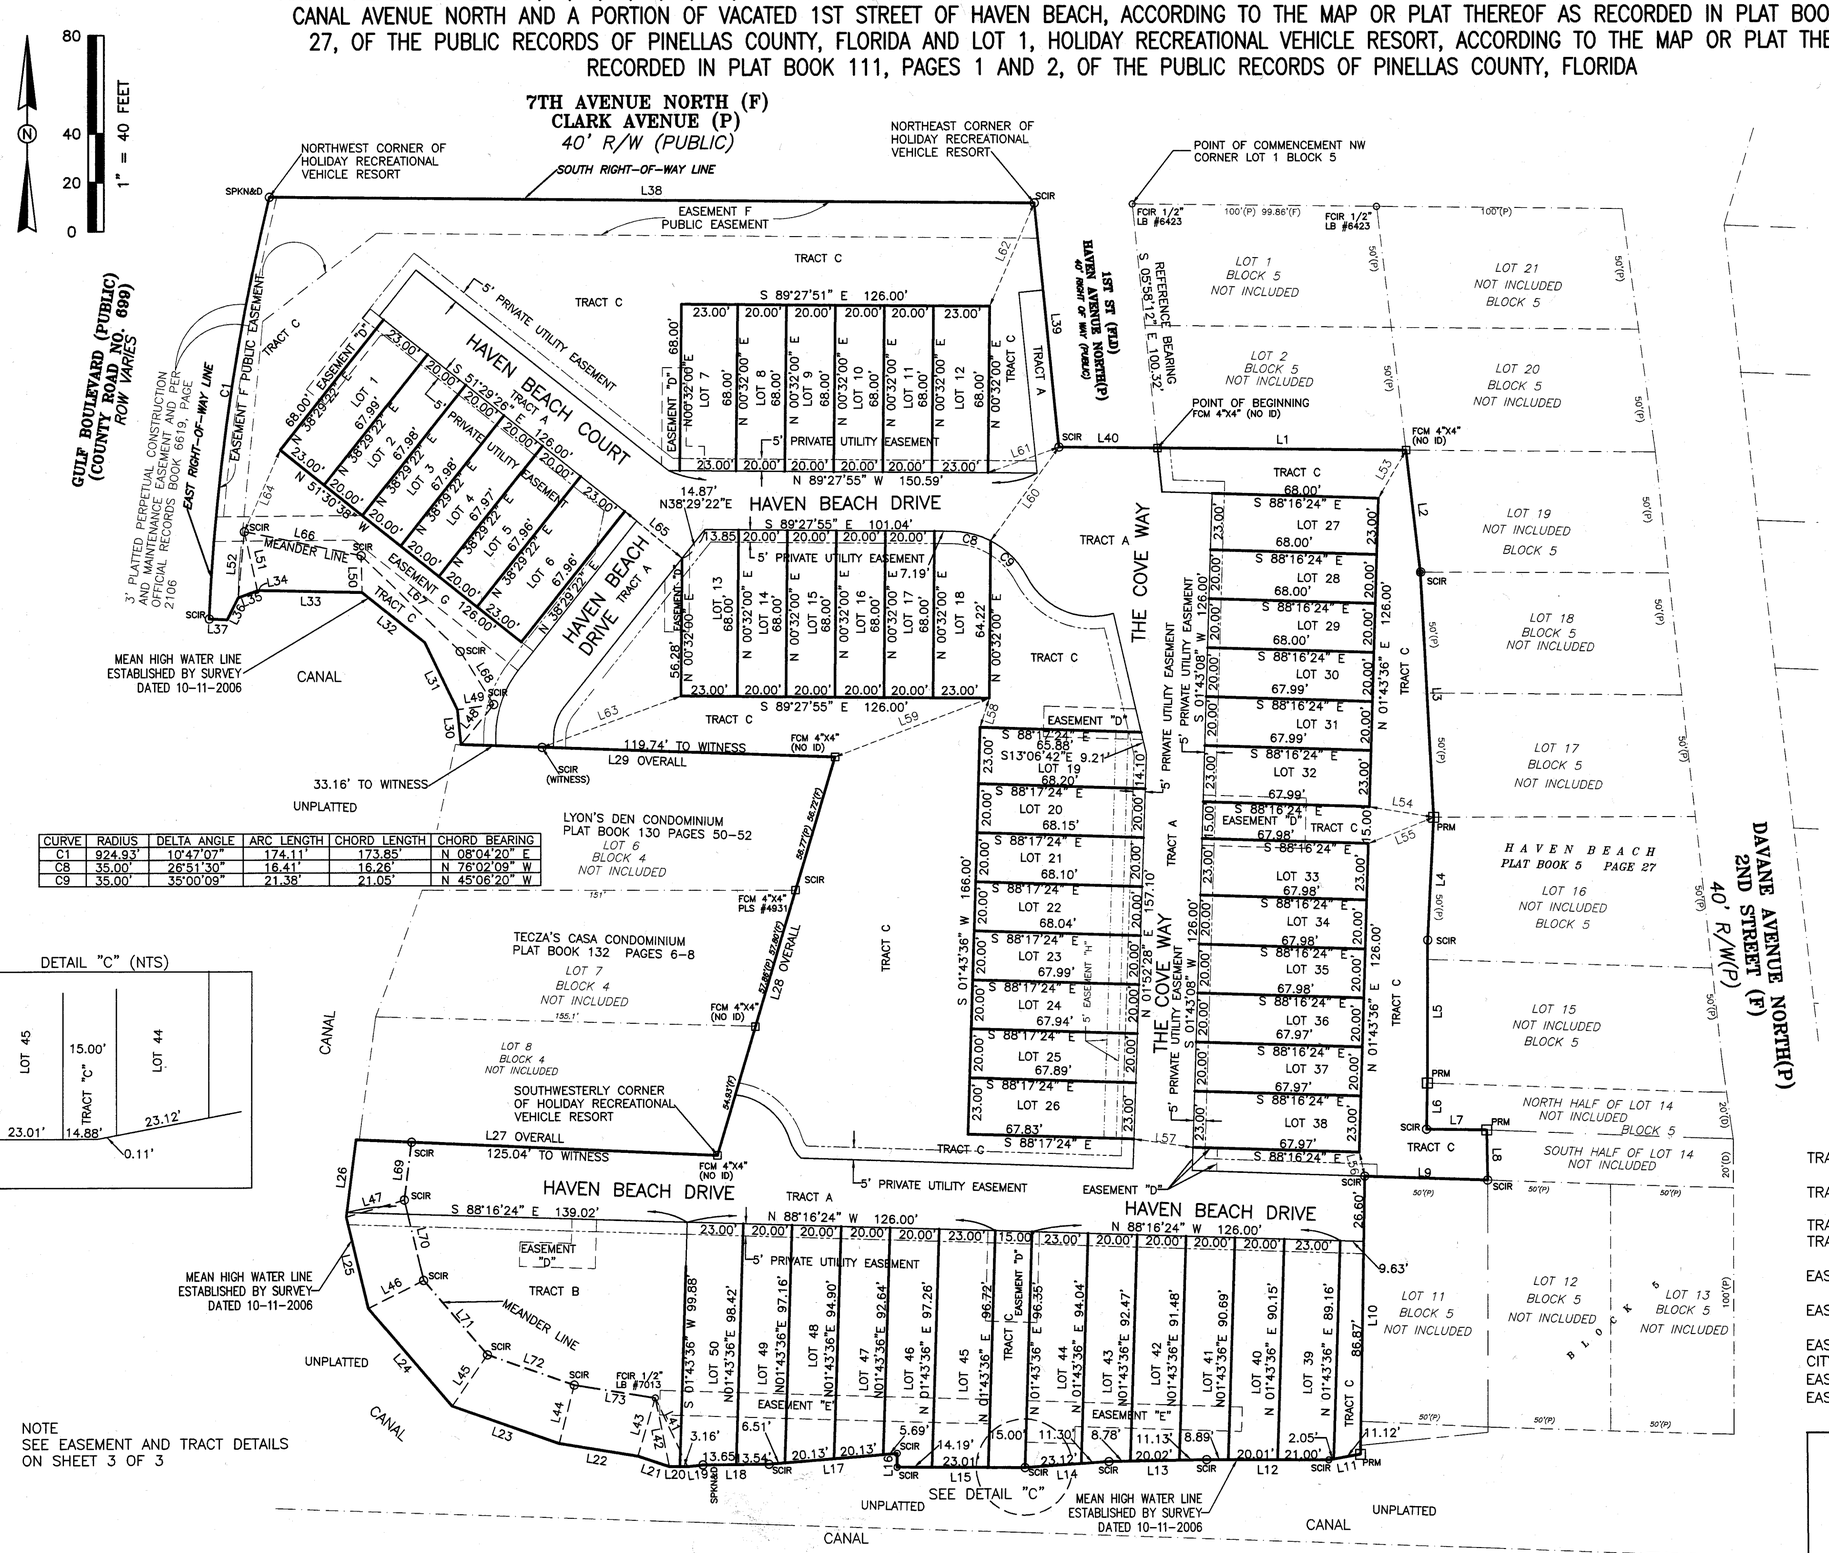

CURVE	RADIUS	DELTA ANGLE	ARC LENGTH	CHORD LENGTH	CHORD BEARING
C1	924.93'	10°47'07"	174.11'	173.85'	N 08°04'20" E
C8	35.00'	26°51'30"	16.41'	16.26'	N 76°02'09" W
C9	35.00'	35°00'09"	21.38'	21.05'	N 45°06'20" W

LINE	BEARING	DISTANCE
L1	S 89°26'28" E	101.61'
L2	S 06°47'56" E	50.13'
L3	S 02°57'59" E	100.23'
L4	S 02°50'26" W	50.06'
L5	S 00°07'38" W	58.27'
L6	S 01°07'41" W	18.93'
L7	S 89°07'49" E	24.57'
L8	S 01°01'49" E	20.48'
L9	N 88°03'06" W	50.19'
L10	S 00°54'26" W	113.47'
L11	S 79°45'27" W	13.17'
L12	N 89°49'10" W	49.89'
L13	S 88°53'50" W	39.93'
L14	S 85°58'36" W	34.53'
L15	N 89°37'51" W	52.08'
L16	N 00°04'49" E	5.60'
L17	S 85°16'51" W	52.46'
L18	S 89°29'58" W	27.19'
L19	S 83°47'20" W	6.27'
L20	N 89°31'44" W	7.48'
L21	N 71°35'18" W	13.44'
L22	N 80°47'00" W	32.61'
L23	N 70°38'55" W	46.32'
L24	N 40°35'43" W	52.60'
L25	N 13°32'22" W	38.42'
L26	N 07°08'39" E	31.78'
L27	S 87°25'45" E	147.78'
L28	N 16°32'57" E	169.45'
L29	N 88°00'51" W	152.90'
L30	N 05°58'10" W	14.35'
L31	N 25°48'14" W	30.60'
L32	N 51°30'39" W	32.73'
L33	N 88°43'36" W	41.75'
L34	S 79°39'01" W	1.04'
L35	S 70°02'58" W	8.33'
L36	S 26°46'54" W	9.92'
L37	N 87°24'46" W	7.39'
L38	S 89°27'18" E	312.56'
L39	S 05°50'19" E	100.31'
L40	S 89°26'28" E	40.27'
L41	S 25°12'32" E	31.02'
L42	S 11°33'51" E	28.58'
L43	S 16°28'24" W	24.77'
L44	S 14°21'14" W	24.66'
L45	S 34°33'49" W	25.46'
L46	S 63°14'42" W	25.34'
L47	S 73°43'00" W	24.70'
L48	S 39°15'25" W	21.13'
L49	S 81°59'27" W	15.01'
L50	S 01°17'56" E	15.01'
L51	S 12°22'34" E	24.71'
L52	S 05°22'07" W	27.10'

LINE	BEARING	DISTANCE
L53	N 30°00'59" E	22.60'
L54	S 80°32'49" E	26.58'
L55	S 68°16'41" W	28.71'
L56	S 13°02'57" E	10.03'
L57	S 81°51'11" E	24.32'
L58	N 17°40'19" E	12.56'
L59	N 69°18'09" E	67.35'
L60	N 36°07'30" E	47.29'
L61	S 70°13'24" W	30.78'
L62	N 23°14'23" E	45.93'
L63	N 69°49'16" E	60.46'
L64	N 23°35'42" E	36.33'
L65	N 50°36'56" W	30.23'
L66	N 78°18'47" W	48.73'
L67	N 46°00'28" W	56.29'
L68	N 32°06'49" W	25.67'
L69	N 07°09'02" E	23.77'
L70	N 13°32'22" W	33.81'
L71	N 40°35'43" W	40.01'
L72	N 70°38'55" W	37.49'
L73	N 80°48'21" W	33.53'

TRACT/EASEMENT LEGEND

TRACT A	PRIVATE TRACT FOR INGRESS/EGRESS, DRAINAGE AND UTILITIES
TRACT B	PRIVATE AMENITY AREA
TRACT C	COMMON AREA FOR DRAINAGE, UTILITIES, PARKING AND PEDESTRIAN TRAVEL
EASEMENT "D"	WATER LINE EASEMENT TO BE CONVEYED TO PINELLAS COUNTY
EASEMENT "E"	PRIVATE WATER EASEMENT FOR DRY WATERLINE
EASEMENT "F"	PUBLIC EASEMENT AS REQUIRED BY THE CITY OF INDIAN ROCKS BEACH
EASEMENT "G"	PRIVATE SANITARY SEWER EASEMENT
EASEMENT "H"	PRIVATE PEDESTRIAN EASEMENT FOR SIDEWALK

NOTE
SEE EASEMENT AND TRACT DETAILS ON SHEET 3 OF 3

LEGEND
- LB LICENSED BUSINESS
- LS LICENSED SURVEYOR
- PS PROFESSIONAL SURVEYOR & MAPPER
- PLS PROFESSIONAL LAND SURVEYOR
- ID IDENTIFICATION
- R/W RIGHT-OF-WAY
- DE DRAINAGE EASEMENT
- FCM FOUND CONCRETE MONUMENT
- ☐ PRM PERMANENT REFERENCE MONUMENT (SET 4"X4" CONCRETE MONUMENT #LB7013)
- O SPKN&D PRM – PERMANENT REFERENCE MONUMENT (SET PK NAIL & DISK #LB7013)
- O SCIR PRM – PERMANENT REFERENCE MONUMENT (SET 1/2" CAPPED IRON ROD #LB7013)
- PUE PUBLIC UTILITY EASEMENT
- NTS NOT TO SCALE
- (P) PLAT
- (F) FIELD

PLAT NOTES

1) THE BEARINGS SHOWN HEREON ARE BASED ON THE WEST BOUNDARY OF LOTS 1 AND 2, BLOCK 5 OF HAVEN BEACH AS RECORDED IN PLAT BOOK 5, PAGE 27, HAVING A BEARING OF S 05°58'12" E.

2) SUBDIVISION PLATS BY NO MEANS REPRESENT A DETERMINATION ON WHETHER PROPERTIES WILL OR WILL NOT FLOOD. LAND WITHIN THE BOUNDARIES OF THIS PLAT MAY OR MAY NOT BE SUBJECT TO FLOODING; THE CITY OF INDIAN ROCKS BEACH, FLORIDA HAS INFORMATION REGARDING FLOODING AND RESTRICTIONS ON DEVELOPMENT.

3) NOTICE: THIS PLAT AS RECORDED IN ITS GRAPHIC FORM, IS THE OFFICIAL DEPICTION OF THE SUBDIVIDED LANDS DESCRIBED HEREIN AND WILL IN NO CIRCUMSTANCES BE SUPPLANTED IN AUTHORITY BY ANY OTHER GRAPHIC OR DIGITAL FORM OF THE PLAT. THERE MAY BE ADDITIONAL RESTRICTIONS THAT ARE NOT RECORDED ON THIS PLAT THAT MAY BE FOUND IN THE PUBLIC RECORDS OF THIS COUNTY.

4) ALL PLATTED UTILITY EASEMENTS WILL PROVIDE THAT SUCH EASEMENTS WILL ALSO BE EASEMENTS FOR THE CONSTRUCTION, INSTALLATION, MAINTENANCE, AND OPERATION OF CABLE TELEVISION SERVICES; PROVIDED, HOWEVER, NO SUCH CONSTRUCTION, INSTALLATION, MAINTENANCE, AND OPERATION OF CABLE TELEVISION SERVICES WILL INTERFERE WITH THE FACILITIES AND SERVICES OF AN ELECTRIC, TELEPHONE, GAS, OR OTHER PUBLIC UTILITY. IN THE EVENT A CABLE TELEVISION COMPANY DAMAGES THE FACILITIES OF A PUBLIC UTILITY, IT SHALL BE SOLELY RESPONSIBLE FOR THE DAMAGES. THIS SECTION SHALL NOT APPLY TO THOSE PRIVATE EASEMENTS GRANTED TO OR OBTAINED BY A PARTICULAR ELECTRIC, TELEPHONE, GAS, OR OTHER PUBLIC UTIL ITY. SUCH CONSTRUCTION, INSTALLATION, MAINTENANCE, AND OPERATION SHALL COMPLY WITH THE NATIONAL ELECTRICAL SAFETY CODE AS ADOPTED BY THE FLORIDA PUBLIC SERVICE COMMISSION.

PREPARED BY:
HAMILTON
ENGINEERING & SURVEYING, INC.
311 NORTH NEWPORT AVENUE
TAMPA, FL 33606 CERTIFICATE OF AUTHORIZATION LB#7013
TEL (813) 250-3535
FAX (813) 250-3636

2014169381
RECORDED IN
PUBLIC RECORDS PINELLAS COUNTY
FL
BK: 139 PG:43-45
06/13/2014 at 04:41 PM.
KEN BURKE, CLERK OF COURT AND COMPTROLLER

SUBDIVISION PLAT
PLAT BOOK: 139 PAGE: 45

PLAT BOOK _____ PAGE _____

COVE AT INDIAN ROCKS BEACH

PORTION OF SECTION 12, TOWNSHIP 30 SOUTH, RANGE 14 EAST,
CITY OF INDIAN ROCKS BEACH, PINELLAS COUNTY, FLORIDA

AND A REPLAT OF LOTS 3, 4, 5, 6, 7, 9, 10, AND A PORTION OF LOTS 8 AND 14, BLOCK 5 AND LOTS 9, 10, 11, 12 AND 13, BLOCK 4 AND A PORTION OF VACATED CANAL AVENUE NORTH AND A PORTION OF VACATED 1ST STREET OF HAVEN BEACH, ACCORDING TO THE MAP OR PLAT THEREOF AS RECORDED IN PLAT BOOK 5, PAGE 27, OF THE PUBLIC RECORDS OF PINELLAS COUNTY, FLORIDA AND LOT 1, HOLIDAY RECREATIONAL VEHICLE RESORT, ACCORDING TO THE MAP OR PLAT THEREOF AS RECORDED IN PLAT BOOK 111, PAGES 1 AND 2, OF THE PUBLIC RECORDS OF PINELLAS COUNTY, FLORIDA

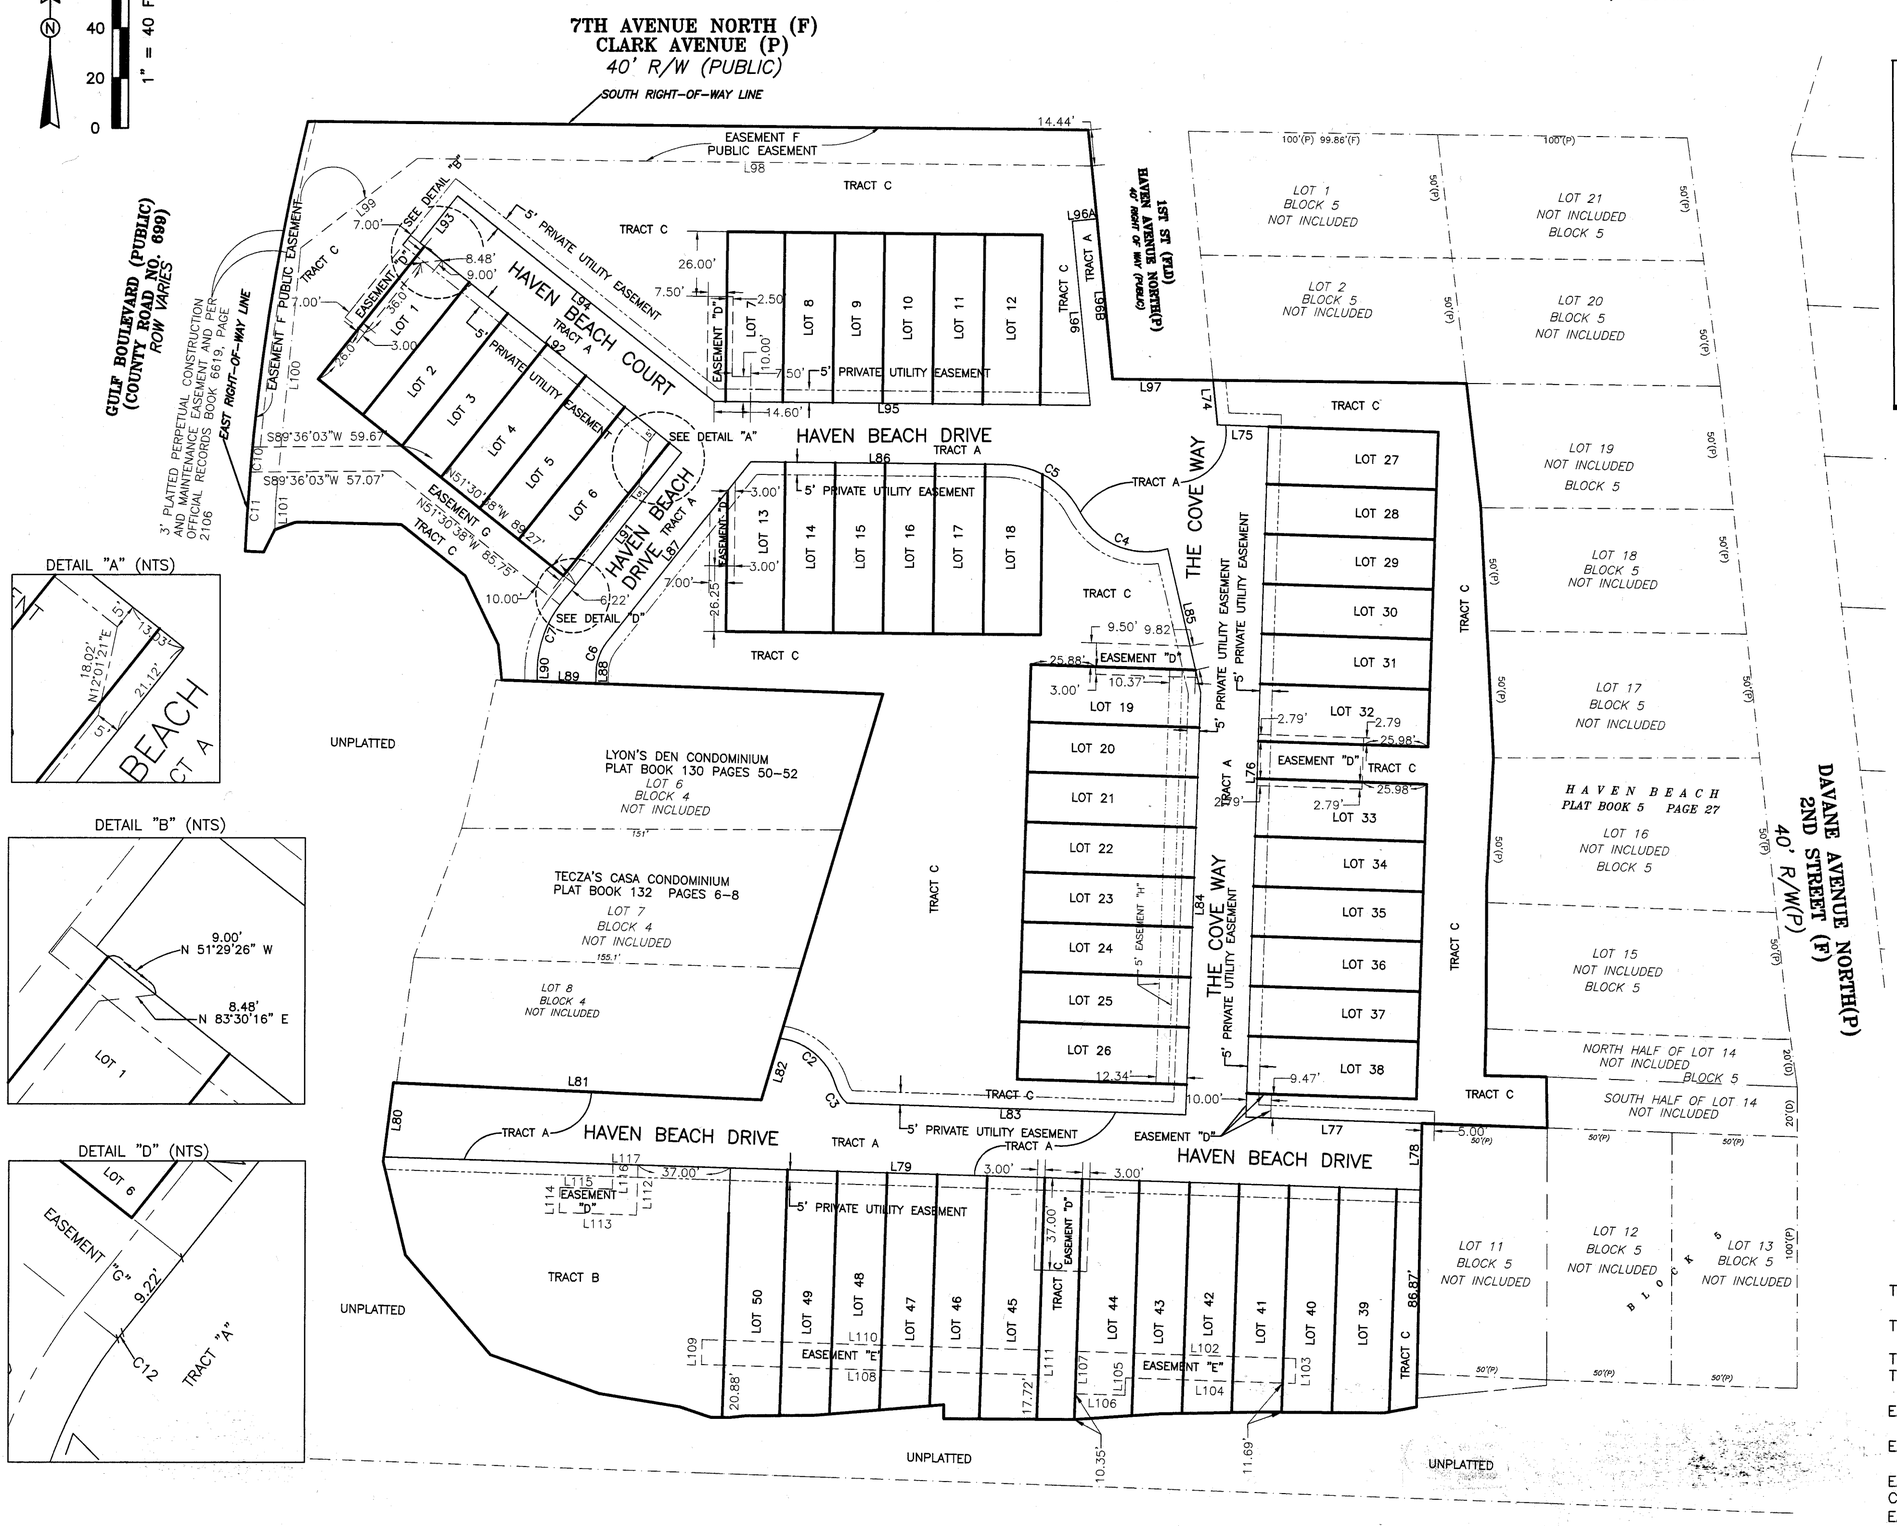

LEGEND
LB LICENSED BUSINESS
LS LICENSED SURVEYOR
PS PROFESSIONAL SURVEYOR & MAPPER
PLS PROFESSIONAL LAND SURVEYOR
ID IDENTIFICATION
R/W RIGHT-OF-WAY
DE DRAINAGE EASEMENT
FCM FOUND CONCRETE MONUMENT
□ PRM PERMANENT REFERENCE MONUMENT (SET 4"X4" CONCRETE MONUMENT #LB7013)
○ SPKN&D PRM – PERMANENT REFERENCE MONUMENT (SET PK NAIL & DISK #LB7013)
○ SCIR PRM – PERMANENT REFERENCE MONUMENT (SET 1/2" CAPPED IRON ROD #LB7013)
PUE PUBLIC UTILITY EASEMENT
NTS NOT TO SCALE
(P) PLAT
(F) FIELD

LINE	BEARING	DISTANCE
L74	S 05°49'48" E	17.98'
L75	S 88°16'24" E	20.51'
L76	S 01°43'08" W	276.44'
L77	S 88°03'52" E	70.52'
L78	S 00°54'26" W	26.60'
L79	N 88°16'24" W	415.65'
L80	N 07°08'39" E	29.88'
L81	S 87°25'45" E	147.78'
L82	N 16°37'51" E	25.74'
L83	S 88°03'52" E	135.61'
L84	N 01°52'28" E	169.17'
L85	N 13°06'42" W	58.98'
L86	N 89°27'55" W	101.04'
L87	S 38°29'22" E	92.34'
L88	S 01°21'19" W	4.65'
L89	N 88°00'51" W	23.51'
L90	N 01°04'04" E	4.78'
L91	N 38°29'22" E	77.17'
L92	N 51°29'26" W	134.49'
L93	N 38°29'22" E	24.00'
L94	S 51°30'38" E	131.84'
L95	S 89°27'55" E	150.59'
L96	N 05°50'19" W	74.14'
L96A	N 84°09'41" E	10.00'
L96B	S 05°50'19" E	64.51'
L97	S 89°26'28" E	40.27'
L98	N 89°28'02" W	270.11'
L99	S 52°17'42" W	58.86'
L100	S 05°22'37" W	102.03'
L101	S 01°45'24" W	11.20'
L102	S 88°16'24" E	88.00'
L103	S 01°43'36" W	10.00'
L104	N 88°16'24" W	68.00'
L105	S 01°43'36" W	7.00'
L106	N 88°16'24" W	20.00'
L107	N 01°43'36" E	17.00'
L108	N 88°16'24" W	135.00'
L109	N 01°43'36" E	10.00'
L110	S 88°16'24" E	135.00'
L111	S 01°43'36" W	10.00'
L112	S 01°43'36" W	20.00'
L113	N 88°16'24" W	30.92'
L114	N 01°43'39" E	10.00'
L115	S 88°16'24" E	20.92'
L116	N 01°43'36" E	10.00'
L117	S 88°16'24" E	10.00'

TRACT/EASEMENT LEGEND

TRACT A	PRIVATE TRACT FOR INGRESS/EGRESS, DRAINAGE AND UTILITIES
TRACT B	PRIVATE AMENITY AREA
TRACT C	COMMON AREA FOR DRAINAGE, UTILITIES, PARKING AND PEDESTRIAN TRAVEL
EASEMENT "D"	WATER LINE EASEMENT TO BE CONVEYED TO PINELLAS COUNTY
EASEMENT "E"	PRIVATE WATER EASEMENT FOR DRY WATERLINE
EASEMENT "F"	PUBLIC EASEMENT AS REQUIRED BY THE CITY OF INDIAN ROCKS BEACH
EASEMENT "G"	PRIVATE SANITARY SEWER EASEMENT
EASEMENT "H"	PRIVATE PEDESTRIAN EASEMENT FOR SIDEWALK

CURVE	RADIUS	DELTA ANGLE	ARC LENGTH	CHORD LENGTH	CHORD BEARING
C2	27.00'	66°05'00"	31.14'	29.44'	S 49°58'58" E
C3	15.00'	31°44'49"	8.31'	8.21'	S 32°48'52" E
C4	30.00'	79°09'16"	41.45'	38.23'	N 67°10'53" W
C5	35.00'	61°51'39"	37.79'	35.98'	N 58°32'05" W
C6	20.00'	37°08'03"	12.96'	12.74'	S 19°55'20" W
C7	44.00'	37°25'17"	28.74'	28.23'	N 19°46'43" E
C10	924.93'	00°37'20"	10.04'	10.04'	N 04°57'18" E
C11	924.93'	01°57'51"	31.71'	31.71'	N 03°39'42" E
C12	44.00'	1°01'02"	0.78'	0.78'	S 37°58'51" W

PREPARED BY:
HAMILTON
ENGINEERING & SURVEYING, INC.
311 NORTH NEWPORT AVENUE
TAMPA, FL 33606 CERTIFICATE OF AUTHORIZATION LB#7013
TEL (813) 250-3535
FAX (813) 250-3636