A 20130

SUN CITY CENTER UNIT-45

RECEIVED
MAY 2 12 58 PM '78
CLERK CIRCUIT COURT
HILLSBOROUGH COUNTY, FLA.

Section 7
Township 32 South
Range 20 East
Hillsborough County, Florida

DESCRIPTION:

A parcel of land lying in the Northeast ¼ of Section 7, Township 32 South, Range 20 East, Hillsborough County, Florida, more particularly described as follows:

Commence at the Southwest corner of the Northeast ¼ of said Section 7; thence N 89°35'44" E, along the South boundary of said Northeast ¼, a distance of 893.66 feet; thence N 00°24'16" W, a distance of 38.15 feet to a point on the North right-of-way line of S. R. No. 674, (said line also being the South right-of-way line of Rickenbacker Drive); thence N 00°46'57" W, a distance of 40.00 feet, to a point on the North right-of-way line of said Rickenbacker Drive; thence N 89°13'03" E, along said North right-of-way line, a distance of 130.00 feet, to a point on the East boundary of Sun City Center Unit No. 34-A, as recorded in Plat Book 48, Page 20, of the Public Records of Hillsborough County, Florida for a Point of Beginning; thence along the Easterly boundary of said Sun City Center Unit No. 34-A, along the following calls and distances:
N 00°46'57" W, 70.00 feet; N 01°24'27" W, 176.98 feet;
N 74°48'33" W, 50.00 feet; N 00°46'57" W, 387.20 feet;
N 37°10'40" W, 300.19 feet; N 00°25'29" W, 170.00 feet;
N 40°36'56" E, 120.32 feet; N 00°25'29" W, 646.25 feet;
thence leaving said Easterly boundary N 85°05'00" E, a distance of 212.09 feet; thence N 56°10'15" E, a distance of 175.83 feet; thence N 89°43'34" E, a distance of 339.22 feet; thence S 23°49'41" E, a distance of 374.16 feet; thence S 08°10'44" W, a distance of 69.31 feet; thence S 00°46'57" E, a distance of 85.00 feet; thence N 89°-13'03" E, a distance of 47.34 feet; thence S 00°46'57" E, a distance of 216.37 feet; thence S 26°25'14" W, a distance of 137.15 feet; thence S 00°46'57" E, a distance of 429.67 feet; thence S 43°-29'17" W, a distance of 79.04 feet; thence S 00°46'57" E, a distance of 102.38 feet, to a Point of Curvature; thence along a curve to the right, on an arc of 206.58 feet, having a radius of 160.00 feet, subtended by a chord of 192.53 feet, chord bearing S 36°12'20" W, to a Point of Reverse Curvature; thence along a curve to the left on an arc of 59.53 feet, having a radius of 50.00 feet, subtended by a chord of 56.08 feet, chord bearing S 39°04'59" W, to a Point of Reverse Curvature; thence along a curve to the right on an arc of 176.95 feet, having a radius of 437.00 feet, subtended by a chord of 175.74 feet, chord bearing S 16°34'21" W, to a Point of Reverse Curvature; thence along a curve to the left on an arc of 83.38 feet, having a radius of 165.00 feet, subtended by a chord of 82.50 feet, chord bearing S 13°41'42" W, to a Point of Tangency; thence S 00°46'57" E, a distance of 35.00 feet, to a point on the North right-of-way line of Rickenbacker Drive; thence S 89°13'03" W, along said right-of-way line, a distance of 75.00 feet to a Point of Curvature; thence along a curve to the right, on an arc of 54.98 feet, having a radius of 35.00 feet, subtended by a chord of 49.50 feet, chord bearing N 45°46'57" W, to a Point of Compound Curvature; thence along a curve to the right, on an arc of 92,05 feet, having a radius of 275.00 feet, subtended by a chord of 91.62 feet, chord bearing N 08°48'23" E, thence N 71°36'17" W, a distance of 50.00 feet, to a point on a curve; thence along a curve to the left, on an arc of 108.78 feet, having a radius of 325.00 feet, subtended by a chord of 108.28 feet, chord bearing S 08°48'23" W, to a Point of Reverse Curvature; thence along a curve to the right, on an arc of 54.98 feet, having a radius of 35.00 feet, subtended by a chord of 49.50 feet, chord bearing S 44°13'03" W, to a Point of Tangency; thence S 89°13'03" W, along the North right-of-way line of Rickenbacker Drive, a distance of 200.00 feet, to the Point of Beginning.

Said parcel contains 31.56 Acres, more or less.

DEDICATION

The undersigned as owner _____ of all the lands platted, hereby dedicate this plat for record and all streets, roads, alleys, rights-of-way, canals, ditches, parks, and other easements shown hereon, to public use this 10TH day of MARCH, 1978, A. D.

OWNER: W.G. DEVELOPMENT CORPORATION

Evelyn K. Colding — WITNESS
Wm J. Durick — WILLIAM J. DURICK VICE PRESIDENT

ACKNOWLEDGMENT
COUNTY OF HILLSBOROUGH
STATE OF FLORIDA

Personally appeared before me the undersigned authority, WILLIAM J. DURICK to me well known and known to me to be the person described in, and who executed the foregoing instrument and separately acknowledged the execution thereof to be their free act and deed for the uses and purposes herein expressed, witness my hand and official seal on this the 10th day of March, 1978, A. D.

Karen S. Mudd — Notary Public, State of Florida
January 18, 1982 — My commission expires

BOARD OF COUNTY COMMISSIONERS
COUNTY OF HILLSBOROUGH
STATE OF FLORIDA

Dedication of streets, roads, alleys, and other rights-of-way accepted and showing of grades and elevations on plat or by separate attached instrument waived by resolution of the Board of County Commissioners, adopted April 26, 1978, A. D. Grades and elevations shown on instruments filed in Office of County Engineer.

Frances M. Davis — Chairman
May 2, 1978 — Date

CLERK OF CIRCUIT COURT
COUNTY OF HILLSBOROUGH
STATE OF FLORIDA

I certify that this plat complies in form with all requirements of Chapter 177, Florida Statutes, filed for record on this the 1st day of May, 1978, A. D. in Plat Book 48, Page 85 of the Public Records of Hillsborough County, Florida.

James F. Taylor, Jr. — Clerk of Circuit Court
Audrey M. Karr — Deputy Clerk

COUNTY ENGINEER

This plat is hereby approved by the County Engineer, Hillsborough County, Florida.

Jimmy D. Allison — County Engineer
5/1/78 — Date

ZONING DIRECTOR

This plat is hereby approved by the Zoning Director, Hillsborough County, Florida.

H W Shaw — Zoning Director
5/2/78 — Date

SURVEYOR'S CERTIFICATE

We certify that the within plat was drawn from a survey made by us in OCTOBER, 1977, A. D., that said plat is a correct representation of the lands platted and that permanent reference monuments have been placed as prescribed by law.

Donald L. Haubino — Florida Reg. Surveyor No. 2242

DELTA ENGINEERING COMPANY
land surveyors civil engineers consultants
3511 4th STREET TAMPA FLORIDA 33610 PHONE 813 626 5481

A 20130

RECEIVED
MAY 2 12 59 PM '78
CLERK OF CIRCUIT COURT
HILLSBOROUGH COUNTY, FLA.

Section 7
Township 32 South
Range 20 East
Hillsborough County, Florida

SUN CITY CENTER UNIT-45

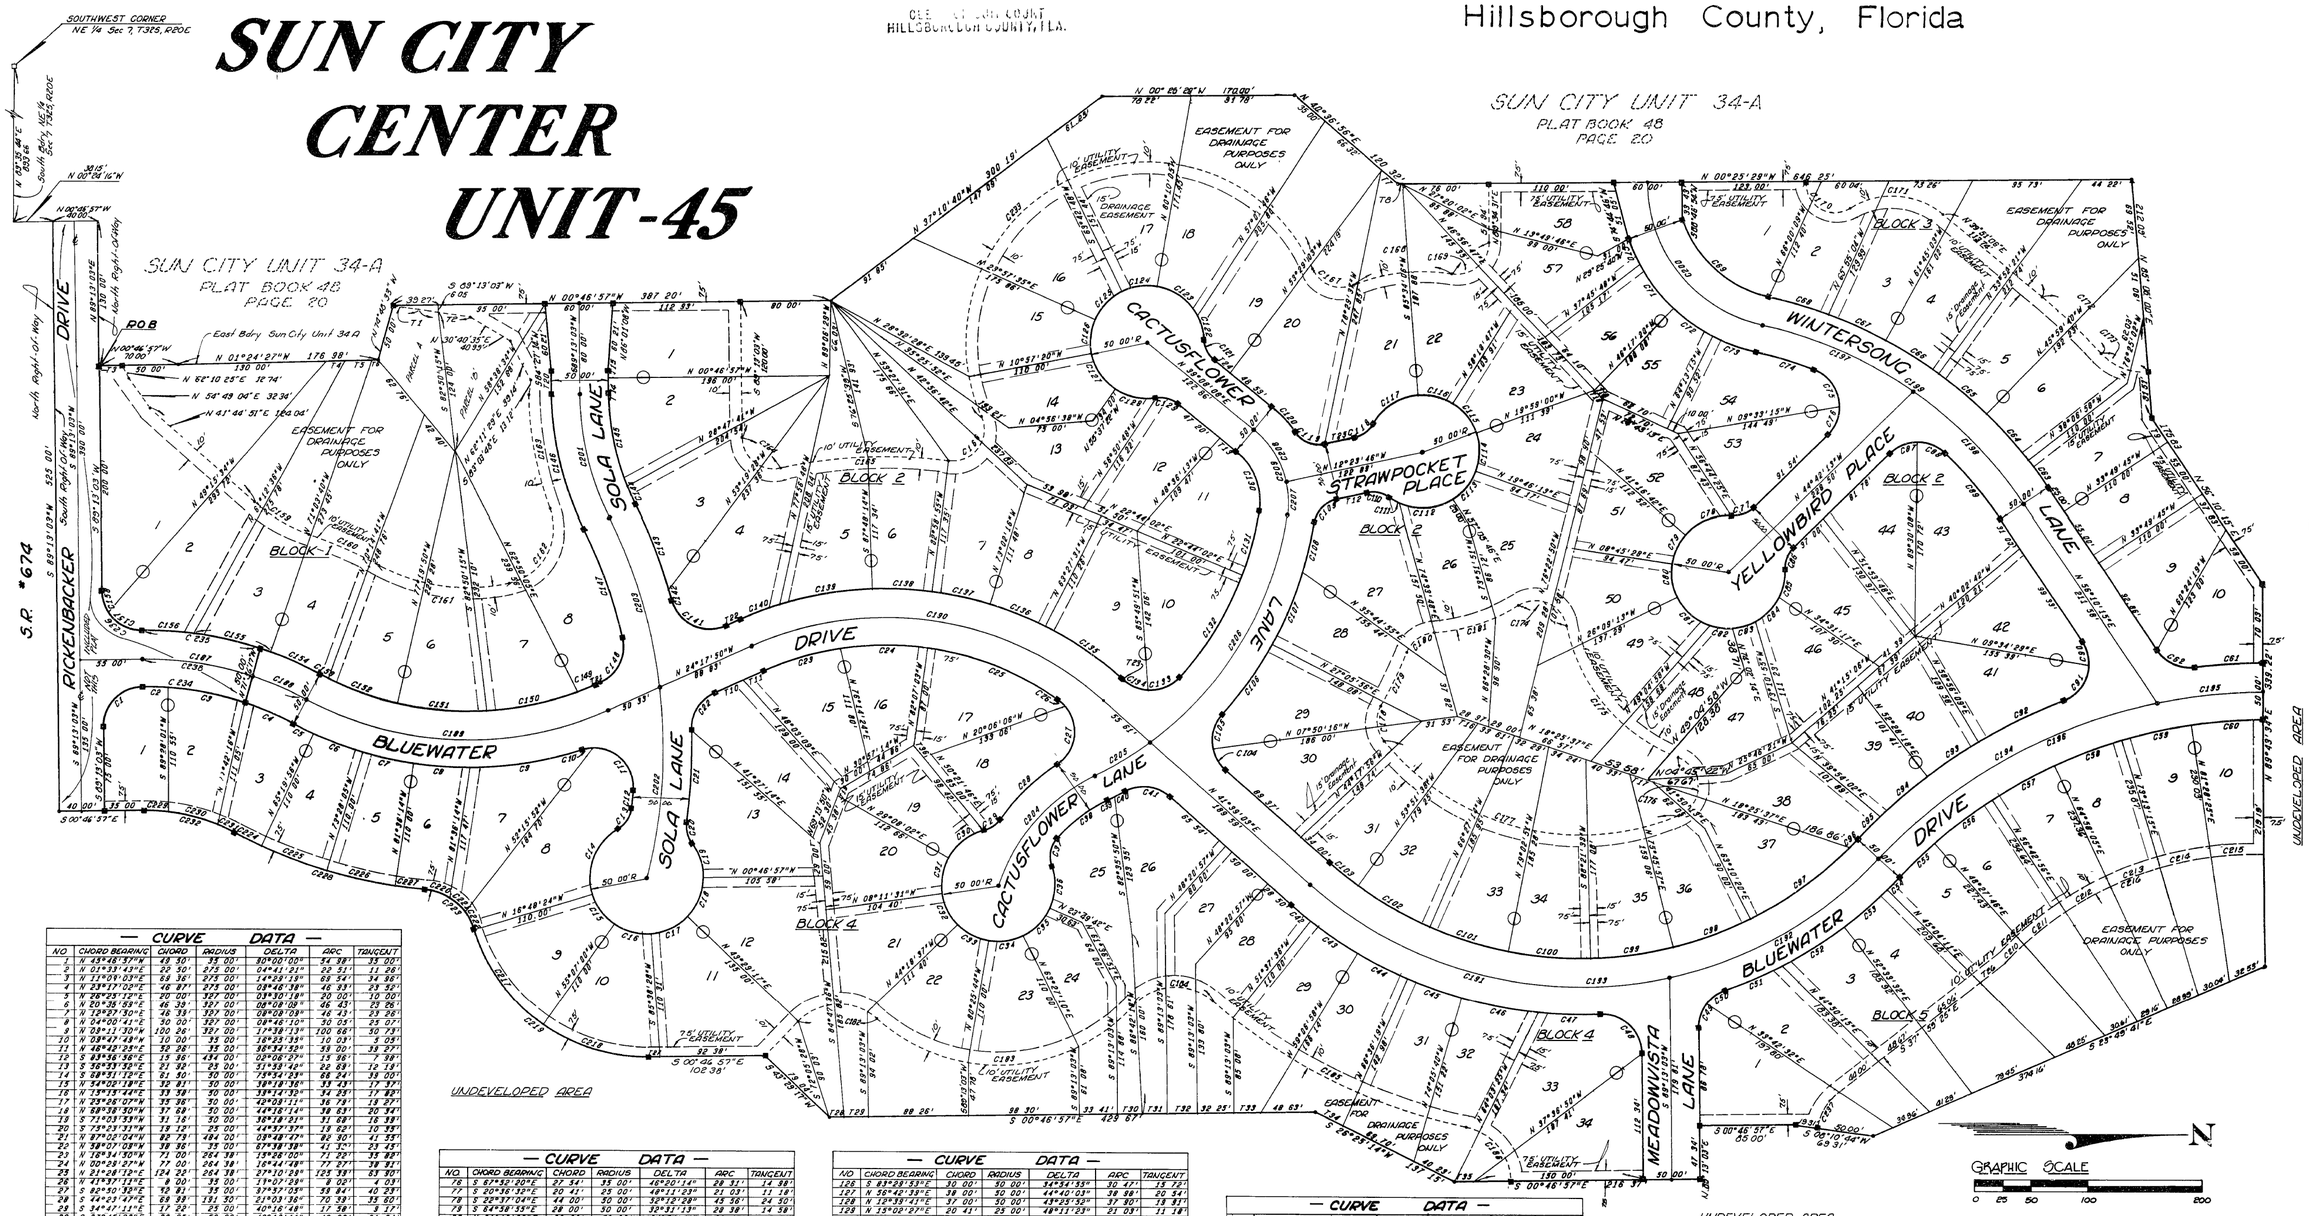

— CURVE DATA —

NO	CHORD BEARING	CHORD	RADIUS	DELTA	ARC	TANGENT
1	N 43°46'57"W	49.50'	35.00'	90°00'00"	54.98'	35.00'
2	N 01°53'42"E	22.50'	275.00'	04°41'21"	22.51'	22.50'
3	N 11°09'03"E	69.36'	275.00'	14°29'19"	69.54'	34.96'
4	N 23°17'02"E	46.87'	275.00'	09°46'39"	46.93'	23.52'
5	N 30°28'12"E	20.00'	327.00'	03°30'18"	20.00'	10.00'
6	N 20°35'59"E	46.39'	327.00'	08°08'09"	46.43'	23.26'
7	N 12°27'50"E	46.39'	327.00'	08°08'09"	46.43'	23.26'
8	N 04°20'41"E	30.00'	327.00'	05°16'10"	30.01'	15.02'
9	N 05°11'30"W	100.26'	327.00'	17°33'13"	100.68'	50.73'
10	N 09°42'49"W	30.00'	327.00'	05°23'39"	30.03'	15.02'
11	N 16°42'23"E	52.28'	33.00'	98°34'52"	59.00'	39.27'
12	S 83°56'56"E	13.36'	494.00'	09°08'57"	13.36'	7.38'
13	N 78°52'52"E	21.92'	33.00'	37°33'42"	22.69'	12.18'
14	S 88°51'12"E	21.50'	50.00'	25°34'21"	22.34'	11.37'
15	N 54°05'18"E	33.91'	50.00'	38°18'36"	33.29'	17.57'
16	N 13°23'44"E	33.38'	50.00'	38°14'35"	33.37'	17.24'
17	N 23°26'07"W	35.38'	50.00'	40°13'11"	35.78'	18.77'
18	N 68°38'30"W	37.58'	50.00'	43°03'14"	38.69'	20.34'
19	S 71°03'53"W	31.16'	50.00'	36°18'21"	31.88'	16.39'
20	S 75°23'31"W	13.72'	25.00'	44°57'37"	13.92'	10.55'
21	N 87°05'02"W	22.79'	494.00'	02°38'26"	22.80'	11.55'
22	N 58°07'09"W	38.36'	33.00'	67°38'38"	41.37'	23.45'
23	N 12°34'30"W	71.00'	264.98'	15°28'00"	71.72'	35.98'
24	N 00°28'57"W	77.00'	264.98'	16°44'18"	77.37'	38.93'
25	N 21°28'12"E	124.22'	264.98'	27°10'29"	125.98'	63.90'
26	N 27°37'13"E	8.00'	35.00'	13°07'39"	8.02'	4.03'
27	S 82°50'35"E	42.81'	35.00'	37°37'05"	39.68'	20.93'
28	S 44°23'47"E	69.99'	131.50'	31°03'36"	70.98'	35.60'
29	S 24°47'13"E	17.23'	25.00'	39°28'48"	17.52'	9.17'
30	S 37°45'23"E	39.23'	50.00'	45°13'11"	40.93'	21.54'
31	S 73°51'44"E	32.00'	50.00'	37°13'33"	32.57'	16.88'
32	N 63°44'58"E	31.00'	50.00'	36°07'08"	31.59'	16.37'
33	N 27°37'43"E	31.00'	50.00'	36°07'06"	31.59'	16.30'
34	N 08°29'17"W	31.00'	50.00'	36°07'06"	31.59'	16.30'
35	N 46°21'34"W	31.89'	50.00'	38°37'37"	31.38'	16.50'
36	N 87°50'17"W	36.92'	50.00'	43°19'39"	37.82'	19.86'
37	N 39°08'54"W	29.30'	25.00'	60°14'09"	26.33'	14.87'
38	N 37°23'43"W	39.44'	141.50'	15°58'04"	39.67'	19.93'
39	N 39°43'39"W	7.50'	533.00'	01°17'26"	7.50'	3.75'
40	N 38°12'50"W	8.74'	533.00'	01°24'36"	8.74'	4.37'
41	N 06°17'54"E	40.50'	35.00'	70°42'18"	43.19'	24.83'
42	N 40°00'49"E	21.90'	392.79'	03°18'40"	21.90'	10.95'
43	N 43°37'49"E	30.00'	392.79'	04°23'21"	30.00'	15.01'
44	N 37°08'32"E	30.00'	392.79'	04°23'21"	30.04'	15.05'
45	N 29°39'07"E	30.00'	392.79'	04°28'31"	30.04'	15.05'
46	N 19°44'09"E	30.00'	392.79'	04°28'31"	30.09'	15.04'
47	N 01°28'39"E	55.00'	392.79'	08°14'22"	55.05'	27.57'
48	N 31°53'13"E	50.31'	35.00'	81°53'30"	56.19'	36.18'
49	N 71°38'30"E	23.00'	35.00'	38°31'51"	23.44'	12.18'
50	N 35°56'23"W	13.86'	35.00'	39°37'26"	20.13'	10.35'
51	N 25°54'00"W	55.00'	392.79'	08°14'22"	55.05'	27.57'
52	N 32°34'13"W	85.00'	392.79'	09°44'27"	85.08'	42.62'
53	N 41°51'09"W	50.00'	392.79'	07°18'31"	50.04'	25.05'
54	N 48°04'36"W	13.31'	392.79'	01°57'13"	13.32'	6.66'
55	N 44°22'49"W	43.49'	437.77'	05°41'09"	43.44'	21.74'
56	N 37°24'38"W	63.00'	437.77'	08°15'10"	63.05'	31.58'
57	N 29°09'28"W	63.00'	437.77'	08°15'10"	63.05'	31.58'
58	N 20°54'20"W	63.00'	437.77'	08°15'10"	63.05'	31.58'
59	N 12°39'12"W	63.00'	437.77'	08°15'10"	63.05'	31.58'
60	N 04°24'01"W	63.00'	437.77'	08°15'10"	63.05'	31.58'
61	S 03°47'50"E	33.96'	487.77'	07°02'53"	60.00'	30.04'
62	S 25°28'28"W	38.83'	38.00'	58°57'37"	39.77'	21.88'
63	S 34°01'33"W	33.38'	400.00'	04°47'14"	33.33'	16.97'
64	S 37°58'44"W	34.86'	400.00'	04°59'42"	34.00'	17.54'
65	S 40°03'55"W	34.86'	400.00'	04°59'42"	34.00'	17.54'
66	S 32°11'18"W	34.86'	400.00'	04°59'42"	34.00'	17.54'
67	S 24°18'39"W	34.86'	400.00'	04°59'42"	34.00'	17.54'
68	S 16°25'55"W	34.86'	400.00'	04°59'42"	34.00'	17.54'
69	S 11°45'08"W	102.64'	103.00'	98°31'08"	101.84'	68.93'
70	N 68°23'10"E	29.51'	135.00'	08°15'09"	29.59'	14.82'
71	N 38°39'37"E	48.00'	135.00'	18°17'21"	48.21'	24.41'
72	N 39°41'39"E	62.50'	135.00'	26°45'35"	62.57'	31.85'
73	N 60°23'08"E	43.44'	135.00'	18°26'03"	43.44'	20.84'
74	N 76°32'03"E	33.39'	350.00'	05°46'37"	33.43'	16.72'
75	N 35°08'02"E	39.00'	35.00'	87°49'01"	41.37'	23.48'

— CURVE DATA —

NO	CHORD BEARING	CHORD	RADIUS	DELTA	ARC	TANGENT
76	S 87°32'53"E	27.54'	35.00'	46°20'14"	28.31'	14.98'
77	S 56°12'36"E	42.50'	35.00'	89°47'23"	47.13'	29.83'
78	S 22°37'04"E	44.00'	30.00'	52°72'28"	43.36'	24.50'
79	S 24°59'55"E	28.00'	30.00'	53°31'13"	29.37'	15.58'
80	N 81°58'08"E	30.00'	30.00'	114°54'41"	30.17'	19.52'
81	N 41°30'48"E	38.00'	30.00'	144°00'09"	38.38'	20.34'
82	N 07°20'21"E	30.00'	30.00'	29°59'59"	30.00'	15.00'
83	N 16°45'09"W	21.23'	30.00'	24°30'35"	21.48'	10.88'
84	N 46°28'30"W	30.00'	30.00'	54°54'39"	30.47'	15.72'
85	N 78°52'52"E	30.00'	30.00'	28°55'12"	30.32'	15.47'
86	N 68°47'34"W	20.41'	25.00'	48°11'23"	21.03'	11.18'
87	N 22°42'44"W	28.37'	35.00'	43°58'37"	28.87'	14.33'
88	N 33°31'22"E	28.50'	35.00'	47°08'24"	28.78'	14.95'
89	N 49°39'13"E	75.61'	390.00'	12°24'06"	75.78'	38.03'
90	N 74°03'38"E	21.50'	39.00'	31°34'27"	21.85'	11.30'
91	S 54°40'57"E	38.91'	35.00'	63°44'43"	40.77'	23.03'
92	S 26°11'14"E	93.94'	487.77'	09°45'39"	93.04'	47.02'
93	S 34°07'50"E	55.00'	487.77'	06°27'50"	55.03'	27.54'
94	S 40°42'03"E	54.00'	487.77'	06°20'47"	54.03'	27.04'
95	S 49°30'39"E	98.50'	487.77'	09°20'54"	98.30'	14.26'
96	S 58°11'39"E	123.18'	276.00'	25°27'00"	124.20'	63.17'
97	S 38°03'32"E	107.98'	332.79'	18°40'24"	108.48'	54.72'
98	S 83°42'14"E	44.44'	35.00'	78°48'48"	48.14'	28.78'
99	S 52°58'08"E	18.00'	277.00'	03°43'38"	18.00'	9.00'
100	S 04°39'23"W	73.00'	332.79'	12°34'36"	73.15'	36.73'
101	S 17°14'58"W	73.00'	332.79'	12°34'36"	73.15'	36.73'
102	S 29°50'34"W	73.00'	332.79'	12°34'36"	73.15'	36.73'
103	S 38°33'49"W	32.00'	332.79'	05°30'43"	32.01'	16.03'
104	S 80°01'54"W	28.07'	35.00'	46°49'42"	28.60'	15.23'
105	N 74°50'38"W	31.50'	35.00'	53°28'15"	32.67'	17.64'
106	N 54°41'40"W	76.48'	333.00'	13°11'19"	76.63'	38.50'
107	N 67°16'49"W	68.50'	333.00'	11°78'48"	68.64'	34.34'
108	N 79°16'39"W	45.00'	333.00'	07°44'55"	45.03'	22.53'
109	N 86°48'28"W	25.18'	25.00'	69°18'18"	26.93'	17.08'
110	N 13°41'55"E	20.41'	25.00'	48°11'23"	21.03'	11.18'
111	N 30°03'19"E	10.00'	50.00'	11°28'42"	10.08'	5.03'
112	N 04°17'49"W	27.89'	50.00'	31°57'09"	28.00'	14.37'
113	N 31°54'00"W	32.00'	50.00'	37°19'33"	32.57'	16.89'
114	S 89°51'37"W	34.00'	50.00'	39°45'13"	34.69'	18.08'
115	S 30°51'06"W	34.00'	50.00'	39°45'13"	34.69'	18.08'
116	S 19°37'39"W	31.00'	50.00'	36°07'06"	31.32'	16.30'
117	S 32°30'31"E	50.07'	50.00'	58°09'15"	49.00'	26.67'
118	S 63°13'43"W	20.41'	25.00'	48°11'23"	21.03'	11.18'
119	S 21°22'58"W	27.80'	25.00'	87°33'26"	29.48'	16.12'
120	S 67°06'55"W	29.55'	105.00'	16°01'39"	29.65'	14.92'
121	S 63°13'43"W	20.41'	25.00'	48°11'23"	21.03'	11.18'
122	S 74°40'39"W	21.93'	30.00'	25°17'09"	22.07'	11.22'
123	S 25°58'09"W	54.00'	30.00'	92°12'24"	48.26'	34.00'
124	S 08°13'38"E	31.00'	30.00'	36°07'06"	31.32'	16.30'
125	S 46°09'48"E	34.00'	30.00'	39°45'13"	34.69'	18.08'

— CURVE DATA —

NO	CHORD BEARING	CHORD	RADIUS	DELTA	ARC	TANGENT
126	S 83°28'53"E	30.00'	30.00'	34°54'39"	30.47'	15.72'
127	N 56°12'36"E	42.50'	30.00'	89°47'23"	48.98'	30.83'
128	N 19°39'41"E	37.00'	30.00'	43°23'53"	37.90'	19.93'
129	N 35°07'37"E	30.41'	25.00'	48°11'23"	21.03'	11.18'
130	N 68°45'19"E	55.34'	55.34'	59°16'51"	57.26'	31.85'
131	S 79°39'39"E	39.94'	283.00'	11°37'18"	39.03'	20.63'
132	S 69°42'17"E	108.00'	283.00'	23°12'09"	107.14'	54.20'
133	S 82°36'10"E	30.00'	35.00'	50°43'14"	31.00'	16.80'
134	S 22°12'49"W	23.30'	35.00'	38°30'38"	23.75'	12.33'
135	S 28°21'41"E	32.00'	35.00'	52°38'39"	32.21'	17.30'
136	S 21°43'06"W	32.50'	314.38'	05°54'43"	32.56'	16.34'
137	S 12°10'21"W	32.50'	314.38'	05°54'43"	32.56'	16.34'
138	S 03°37'36"W	32.50'	314.38'	05°54'43"	32.56'	16.34'
139	S 09°48'39"E	33.50'	314.38'	13°13'46"	33.75'	16.92'
140	S 20°59'21"E	37.50'	314.38'	06°50'18"	37.52'	18.78'
141	S 24°39'39"E	53.08'	35.00'	88°54'40"	60.28'	40.68'
142	S 79°41'19"W	10.08'	484.00'	01°11'19"	10.08'	5.04'
143	S 80°50'59"W	81.30'	484.00'	09°38'34"	81.60'	40.90'
144	S 65°40'49"W	12.71'	236.00'	04°53'13"	12.71'	6.36'
145	S 78°34'19"W	83.50'	236.00'	21°17'09"	83.98'	42.49'
146	N 78°11'39"E	123.18'	276.00'	25°27'00"	124.20'	63.17'
147	N 70°08'43"E	101.68'	434.00'	13°27'18"	101.92'	51.19'
148	S 83°42'14"E	44.44'	35.00'	78°48'48"	48.14'	28.78'
149	S 52°58'08"E	18.00'	277.00'	03°43'38"	18.00'	9.00'
150	S 12°02'10"E	82.24'	277.00'	17°04'28"	82.55'	41.58'
151	S 04°51'06"W	73.50'	277.00'	15°30'04"	73.78'	40.37'
152	S 15°44'24"W	84.00'	277.00'	15°58'33"	83.73'	42.35'
153	S 27°19'31"W	8.19'	277.00'	01°41'40"	8.19'	4.10'
154	S 32°50'08"W	48.00'	325.00'	08°28'27"	48.04'	24.08'
155	S 13°30'58"W	70.00'	325.00'	12°20'43"	70.14'	35.24'
156	S 09°16'39"W	46.00'	325.00'	08°08'59"	46.04'	23.08'
157	S 28°25'38"W	55.00'	325.00'	09°42'01"	55.06'	27.59'
158	S 43°26'13"W	13.23'	35.00'	21°52'53"	13.48'	10.00'
159	N 30°29'19"E	56.62'	145.00'	22°31'06"	56.99'	28.87'
160	N 31°26'39"W	57.37'	325.00'	08°58'35"	57.45'	28.79'
161	N 07°43'36"E	116.67'	167.00'	40°53'31"	118.18'	62.26'
162	N 61°12'36"E	44.00'	50.00'	37°57'14"	45.41'	37.47'
163	N 29°15'19"W	103.54'	236.00'	25°13'55"	105.78'	53.80'
164	N 34°19'30"W	43.46'	98.00'	101°48'37"	43.75'	34.46'
165	N 34°19'30"W	123.00'	98.00'	144°00'00"	149.73'	95.53'
166	N 33°28'13"W	48.86'	98.00'	121°30'27"	93.98'	50.01'
167	N 21°39'09"E	38.99'	98.00'	88°14'39"	43.13'	27.16'
168	N 06°38'40"W	24.00'	160.00'	15°13'18"	24.02'	12.06'
169	N 40°37'[illegible]"W	42.78'	98.00'	39°38'30"	42.68'	33.14'
170	N 37°32'08"E	43.01'	25.00'	128°18'58"	55.99'	51.62'
171	N 03°36'52"E	85.01'	68.37'	72°52'58"	87.77'	50.84'
172	N 43°53'58"E	12.00'	510.00'	08°05'44"	12.06'	16.09'
173	N 29°50'58"E	14.52'	39.00'	53°21'50"	16.73'	9.04'
174	N 22°51'12"E	45.93'	28.00'	110°12'47"	60.13'	40.53'
175	N 49°39'26"E	152.22'	160.00'	58°48'33"	158.94'	86.53'

— CURVE DATA —

NO	CHORD BEARING	CHORD	RADIUS	DELTA	ARC	TANGENT
176	N 83°13'00"E	51.81'	28.00'	135°53'41"	66.43'	69.18'
177	S 14°08'39"W	287.93'	200.00'	73°55'39"	287.46'	167.67'
178	S 84°39'53"W	33.13'	97.00'	19°57'01"	33.13'	16.77'
179	N 64°31'43"W	52.81'	443.00'	06°50'08"	52.84'	26.45'
180	N 57°39'19"W	29.69'	443.00'	04°03'09"	29.70'	14.87'
181	N 13°01'49"W	74.07'	180.00'	23°34'39"	74.87'	40.25'
182	N 09°14'00"W	89.81'	30.00'	89°38'47"	77.37'	49.75'
183	N 03°06'10"W	289.82'	180.00'	90°18'09"	285.00'	180.77'
184	N 03°33'46"W	70.31'	30.00'	89°23'17"	77.98'	49.44'
185	N 26°25'14"E	250.00'	488.28'	29°33'16"	252.76'	129.23'
186	N 50°29'13"E	62.53'	50.00'	77°03'37"	67.62'	40.13'
187	N 08°49'53"E	59.95'	300.00'	19°10'40"	100.41'	50.68'
188	N 23°17'02"E	33.13'	300.00'	09°48'39"	33.11'	25.85'
189	N 09°08'10"E	142.83'	300.00'	27°16'31"	142.83'	72.87'
190	N 09°40'56"E	333.00'	288.38'	69°36'34"	333.08'	187.74'
191	N 14°38'06"E	308.79'	333.00'	54°07'14"	333.33'	183.63'
192	N 29°37'16"W	337.79'	337.79'	90°00'00"	315.67'	111.32'
193	N 09°47'09"W	301.00'	337.79'	89°39'28"	334.55'	330.83'
194	N 23°52'24"E	289.23'	337.79'	49°07'13"	289.23'	153.67'
195	N 06°03'15"W	33.21'	462.77'	11°33'39"	33.27'	16.85'
196	N 29°41'39"W	368.08'	462.77'	45°56'57"	378.20'	200.37'
197	N 23°38'33"E	145.00'	325.00'	25°17'41"	145.93'	73.89'
198	N 43°28'46"E	139.14'	325.00'	24°23'00"	139.35'	70.80'
199	N 34°13'33"E	278.00'	325.00'	49°00'41"	285.87'	150.29'
200	S 57°03'03"W	105.58'	325.00'	18°37'39"	105.58'	53.26'
201	S 78°13'39"W	115.00'	231.00'	28°47'00"	112.85'	57.45'
202	S 48°11'39"W	57.37'	308.00'	10°41'37"	57.83'	28.97'
203	S 73°16'42"W	196.59'	308.00'	44°48'46"	240.80'	126.88'
204	N 48°58'21"W	129.50'	166.50'	45°46'15"	133.01'	70.28'
205	N 31°26'39"W	57.37'	308.00'	10°41'37"	57.83'	28.97'
206	N 59°13'08"W	404.46'	308.00'	44°48'46"	240.80'	126.88'
207	S 87°58'15"W	29.20'	60.38'	20°46'28"	29.36'	14.85'
208	S 08°22'04"W	53.38'	80.38'	38°01'38"	54.91'	28.61'
209	S 64°05'19"W	60.05'	60.38'	59°16'51"	63.73'	46.04'
210	N 44°24'39"E	31.60'	318.37'	09°31'09"	31.61'	15.83'
211	N 24°31'18"W	13.42'	318.37'	04°33'12"	13.42'	6.71'
212	N 29°03'39"W	43.85'	318.37'	08°13'10"	43.88'	22.00'
213	N 20°53'30"W	43.85'	318.37'	08°13'10"	43.88'	22.00'
214	N 12°39'10"W	43.85'	318.37'	08°13'10"	43.88'	22.00'
215	N 04°24'01"W	43.85'	318.37'	08°13'10"	43.88'	22.00'
216	N 23°46'34"W	253.80'	318.37'	46°56'57"	261.04'	138.38'
217	N 54°08'18"E	105.00'	160.00'	38°18'36"	106.98'	55.58'
218	N 17°03'02"E	90.00'	160.00'	35°59'33"	90.60'	51.47'
219	N 36°12'00"W	192.00'	160.00'	73°58'33"	206.57'	120.32'
220	N 18°57'23"E	24.17'	30.00'	27°38'14"	24.41'	12.43'

— CURVE DATA —

NO	CHORD BEARING	CHORD	RADIUS	DELTA	ARC	TANGENT
221	N 43°53'46"E	77.70'	50.00'	90°38'21"	79.84'	51.11'
222	N 63°12'18"E	17.90'	50.00'	19°48'40"	17.98'	9.13'
223	N 39°02'39"E	36.00'	50.00'	69°37'15"	36.53'	21.77'
224	N 26°55'12"E	26.73'	437.00'	03°30'18"	26.73'	13.37'
225	N 20°33'39"E	62.00'	437.00'	08°08'09"	62.05'	31.08'
226	N 12°27'30"E	62.00'	437.00'	08°08'09"	62.05'	31.08'
227	N 06°41'04"E	54.11'	437.00'	08°53'53"	54.15'	27.08'
228	N 15°34'16"E	173.29'	437.00'	23°13'00"	174.93'	89.70'
229	N 03°02'33"E	52.25'	165.00'	01°33'22"	52.07'	13.09'
230	N 14°51'17"E	44.93'	165.00'	15°37'00"	44.97'	22.63'
231	N 23°20'24"E	16.39'	165.00'	05°42'14"	16.39'	8.18'
232	N 13°41'42"E	83.30'	165.00'	29°47'14"	83.39'	42.71'
233	N 24°13'23"W	300.00'	180.00'	100°00'00"	305.04'	OS
234	N 08°46'53"E	31.62'	275.00'	06°35'02"	31.62'	15.83'
235	S 08°46'53"W	108.56'	325.00'	19°10'40"	108.78'	54.97'
236	S 44°13'23"W	49.50'	35.00'	90°00'00"	54.98'	35.00'
237	S 58°54'20"E	37.38'	50.00'	42°48'51"	38.20'	20.07'
238	N 13°41'42"E	150.00'	300.00'	28°57'18"	151.61'	77.46'

— TANGENTS —

NO	BEARINGS	DIST
1	N 07°53'52"E	22.61'
2	N 09°25'00"E	46.39'
3	N 00°46'57"W	20.00'
4	N 01°53'42"W	13.07'
5	N 01°24'27"W	94.00'
6	N 01°24'27"W	5.92'
7	N 00°28'57"E	13.06'
8	N 00°28'57"W	4.00'
9	N 36°20'13"E	23.00'
10	N 24°17'30"W	27.73'
11	N 24°17'30"W	19.00'
12	N 24°23'46"W	28.87'
13	N 38°08'08"E	13.76'
14	N 38°13'03"W	14.00'
15	N 38°13'03"W	6.00'
16	N 38°13'03"W	13.33'
17	N 38°29'57"W	27.67'
18	N 48°58'47"E	10.68'
19	N 69°13'50"W	6.92'
20	S 69°13'50"E	6.92'
21	N 24°17'50"W	3.80'
22	N 24°17'50"W	13.58'
23	N 24°17'50"W	28.87'
24	N 38°08'08"E	18.00'
25	N 38°08'08"E	26.87'
26	N 37°53'24"E	27.00'
27	N 00°46'57"W	10.00'
28	N 00°46'57"W	22.00'
29	N 00°46'57"W	31.73'
30	N 00°46'57"W	39.04'
31	N 00°46'57"W	22.00'
32	N 00°46'57"W	36.78'
33	N 00°46'57"W	38.33'
34	N 26°23'14"E	27.22'
35	N 00°46'57"W	34.98'
36	N 30°21'48"E	23.48'

NOTE:

1. IN ADDITION TO EASEMENTS SHOWN ON THIS PLAT, TEN (10) FEET ADJACENT TO BOTH SIDES OF RIGHT-OF-WAY IS RESERVED AS A UTILITY EASEMENT
2. SYMBOL ■ INDICATES PERMANENT REFERENCE MONUMENT (P.R.M.)
3. SYMBOL ● INDICATES PERMANENT CONTROL POINT (P.C.P.)
4. SYMBOL —⊖— INDICATES ZERO LOT LINE FOR EACH DWELLING UNIT
5. A 7.5 FOOT EASEMENT ADJACENT TO BOTH SIDES OF ANY LOT LINE WHICH IS NOT A ZERO LOT LINE IS RESERVED FOR DRAINAGE AND UTILITY PURPOSES

DELTA ENGINEERING COMPANY
LAND SURVEYORS – CIVIL ENGINEERS – CONSULTANTS