LONGLEAF NEIGHBORHOOD TWO
PHASE ONE AND PHASE THREE

BEING A SUBDIVISION OF LAND LYING WITHIN SECTION 19, TOWNSHIP 26 SOUTH, RANGE 17 EAST, PASCO COUNTY, FLORIDA

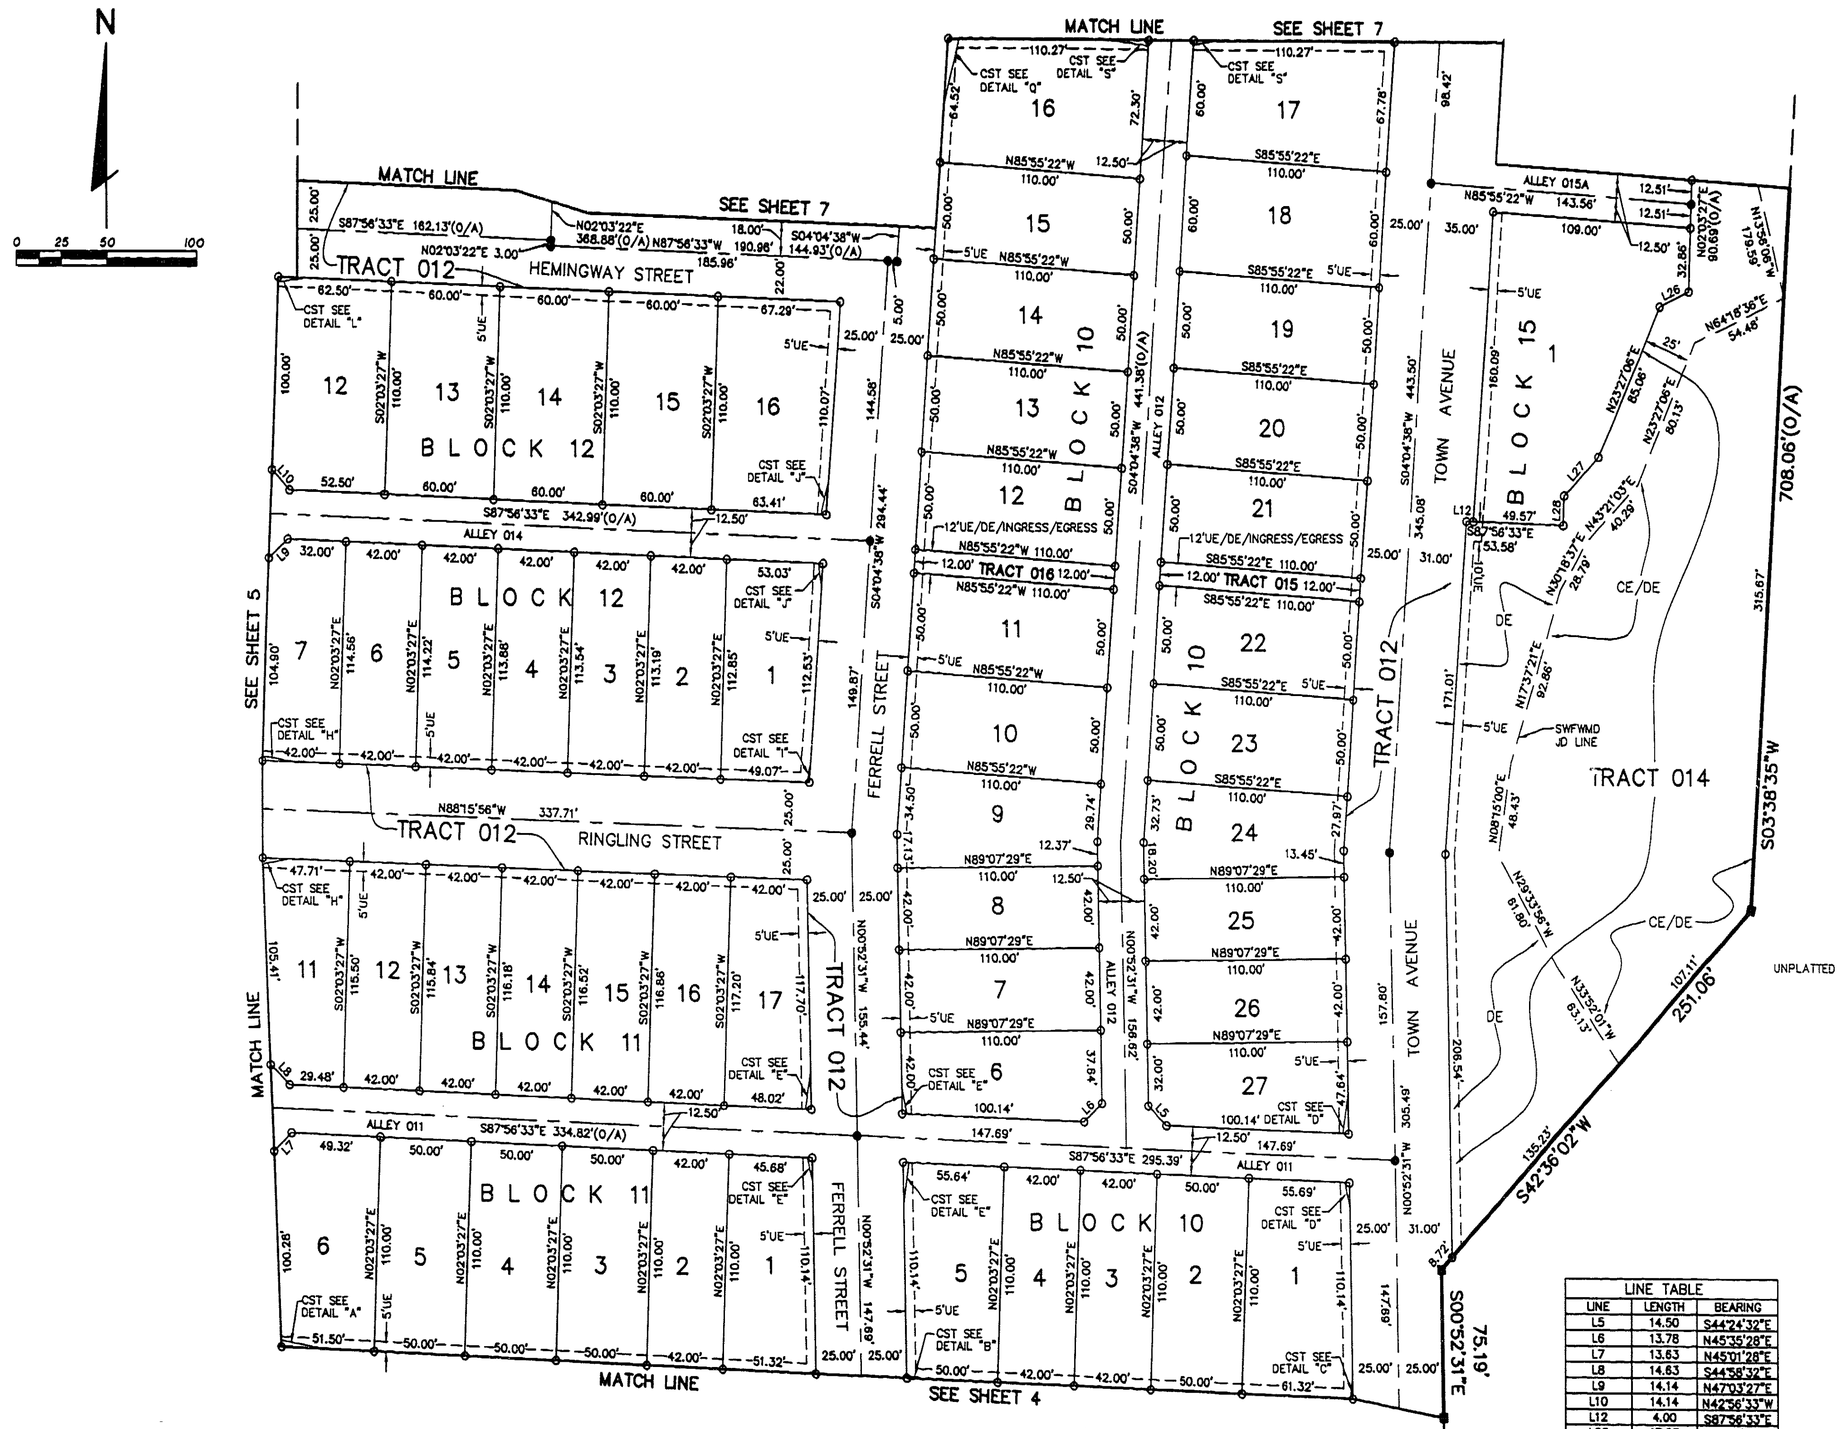

LINE TABLE		
LINE	LENGTH	BEARING
L5	14.50	S44°24'32"E
L6	13.78	N45°35'28"E
L7	13.63	N45°01'28"E
L8	14.63	S44°58'32"E
L9	14.14	N47°03'27"E
L10	14.14	N42°56'33"W
L12	4.00	S87°56'33"E
L26	17.93	S64°18'36"W
L27	27.43	S43°21'03"W
L28	15.15	S02°03'27"W

FLORIDA DESIGN CONSULTANTS, INC.
ENGINEERS, ENVIRONMENTALISTS, SURVEYORS & PLANNERS
6321 Grand Boulevard, New Port Richey FL 34652
Tel. (727) 849-7588 - Fax. (727) 848-3648
Certificate of Authorization: LB 6707
State of Florida

SEE SHEET 3 FOR LEGEND
SEE SHEET 4 FOR NOTES
SEE SHEET 11 FOR CLEAR SIGHT TRIANGLE DETAILS

NOTE:
This plat, as recorded in its graphic form, is the official depiction of the subdivided lands described herein and will in no circumstance be supplanted in authority by any other graphic or digital form of the plat.
There may be additional restrictions that are not recorded on this plat that may be found in the Public Records of this County.