LONGLEAF NEIGHBORHOOD TWO
PHASE ONE AND PHASE THREE

BEING A SUBDIVISION OF LAND LYING WITHIN SECTION 19, TOWNSHIP 26 SOUTH, RANGE 17 EAST, PASCO COUNTY, FLORIDA

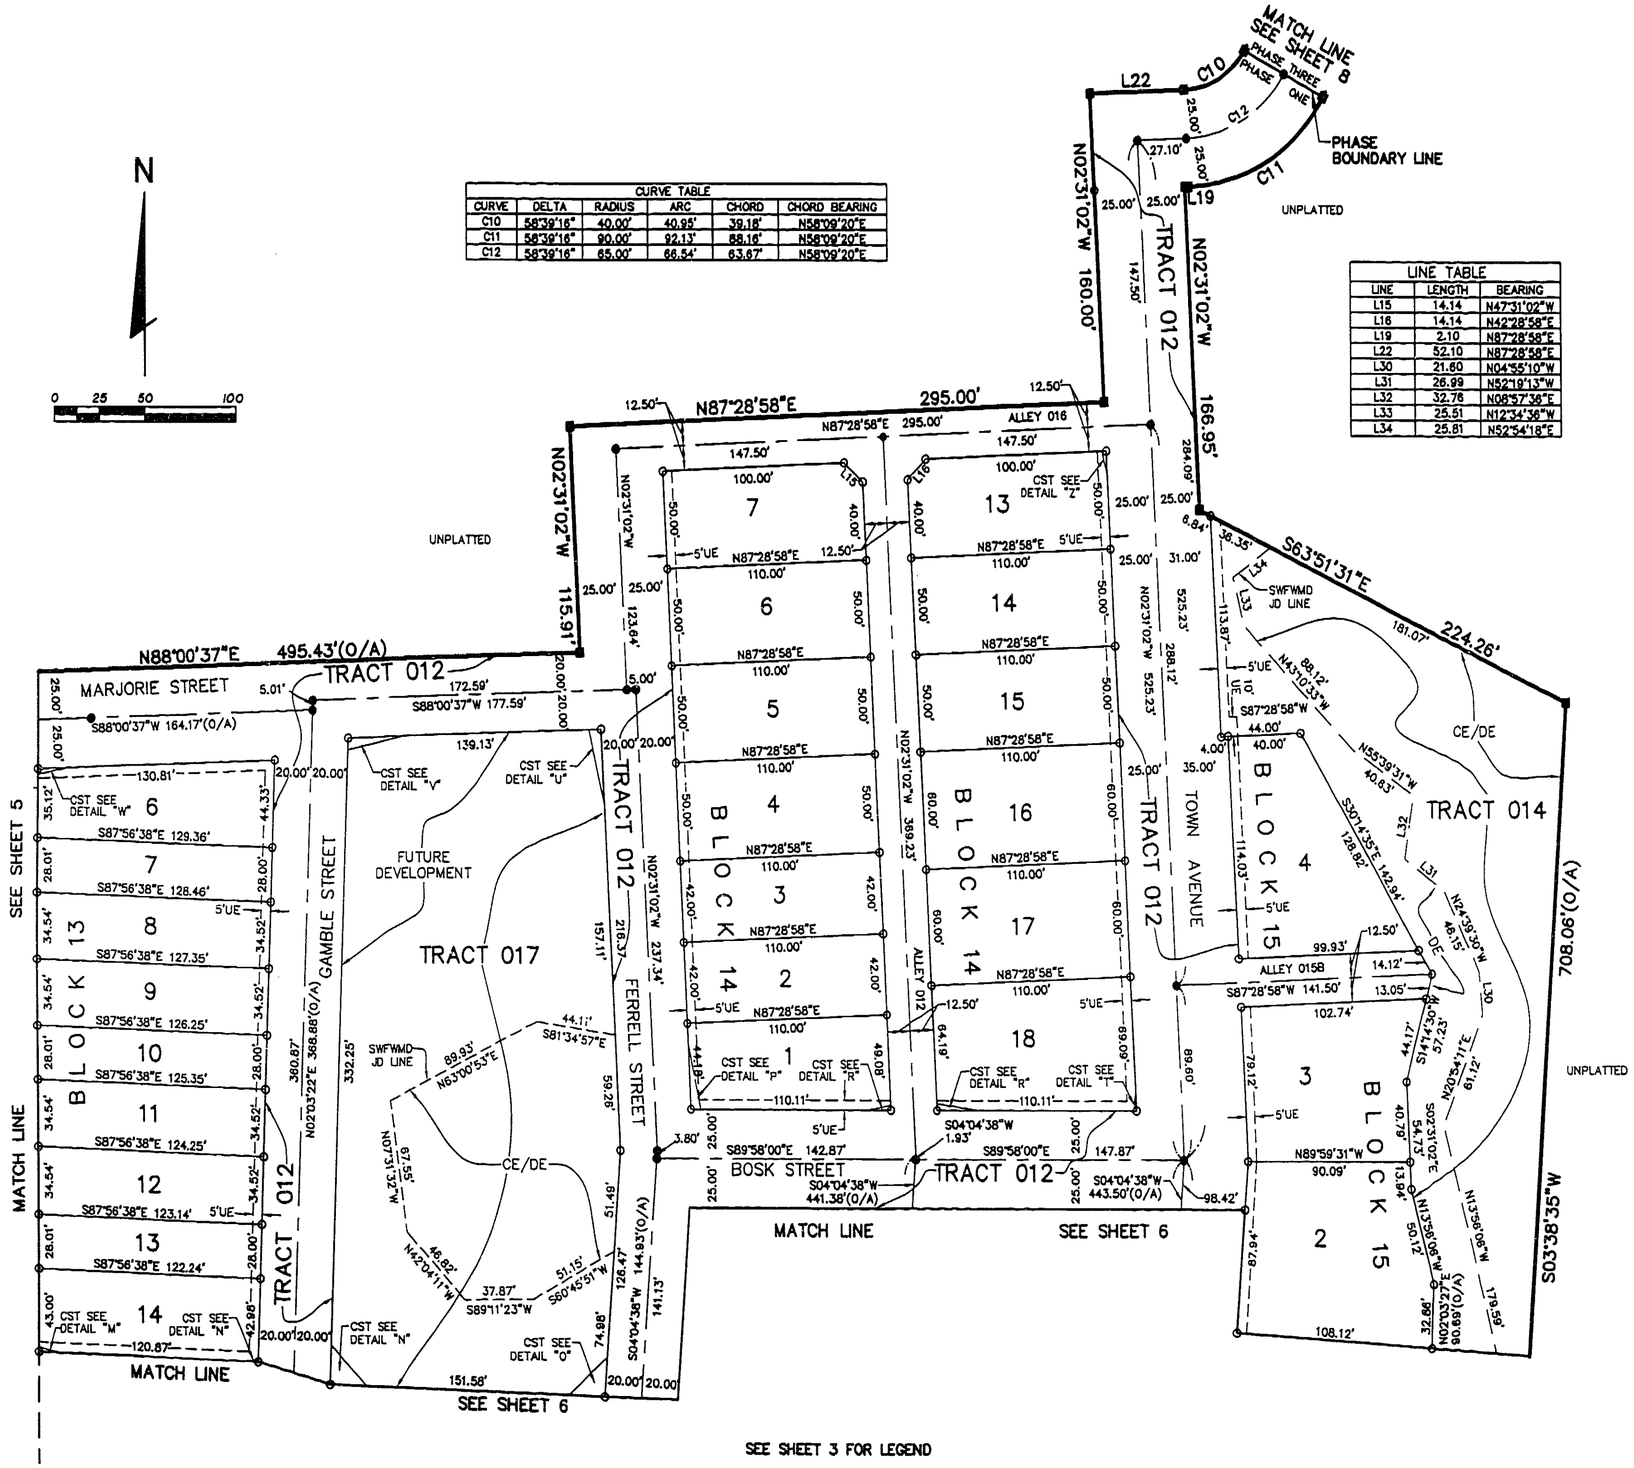

CURVE TABLE					
CURVE	DELTA	RADIUS	ARC	CHORD	CHORD BEARING
C10	58°39'16"	40.00'	40.95'	39.18'	N58°09'20"E
C11	58°39'16"	90.00'	92.13'	88.16'	N58°09'20"E
C12	58°39'16"	65.00'	66.54'	63.67'	N58°09'20"E

LINE TABLE		
LINE	LENGTH	BEARING
L15	14.14	N47°31'02"W
L16	14.14	N42°28'58"E
L19	2.10	N87°28'58"E
L22	52.10	N87°28'58"E
L30	21.60	N04°55'10"W
L31	26.99	N52°19'13"W
L32	32.76	N08°57'36"E
L33	25.51	N12°34'36"W
L34	25.81	N52°54'18"E

SEE SHEET 3 FOR LEGEND

SEE SHEET 4 FOR NOTES

SEE SHEET 11 FOR CLEAR SIGHT TRIANGLE DETAILS

FLORIDA DESIGN CONSULTANTS, INC.
ENGINEERS, ENVIRONMENTALISTS, SURVEYORS & PLANNERS
6321 Grand Boulevard, New Port Richey FL 34652
Tel: (727) 849-7588 - Fax: (727) 848-3648
Certificate of Authorization: LB 6707
State of Florida

NOTE:
This plat, as recorded in its graphic form, is the official depiction of the subdivided lands described herein and will in no circumstance be supplanted in authority by any other graphic or digital form of the plat.
There may be additional restrictions that are not recorded on this plat that may be found in the Public Records of this County.