LONGLEAF NEIGHBORHOOD TWO
PHASE ONE AND PHASE THREE

BEING A SUBDIVISION OF LAND LYING WITHIN SECTION 19, TOWNSHIP 26 SOUTH, RANGE 17 EAST, PASCO COUNTY, FLORIDA

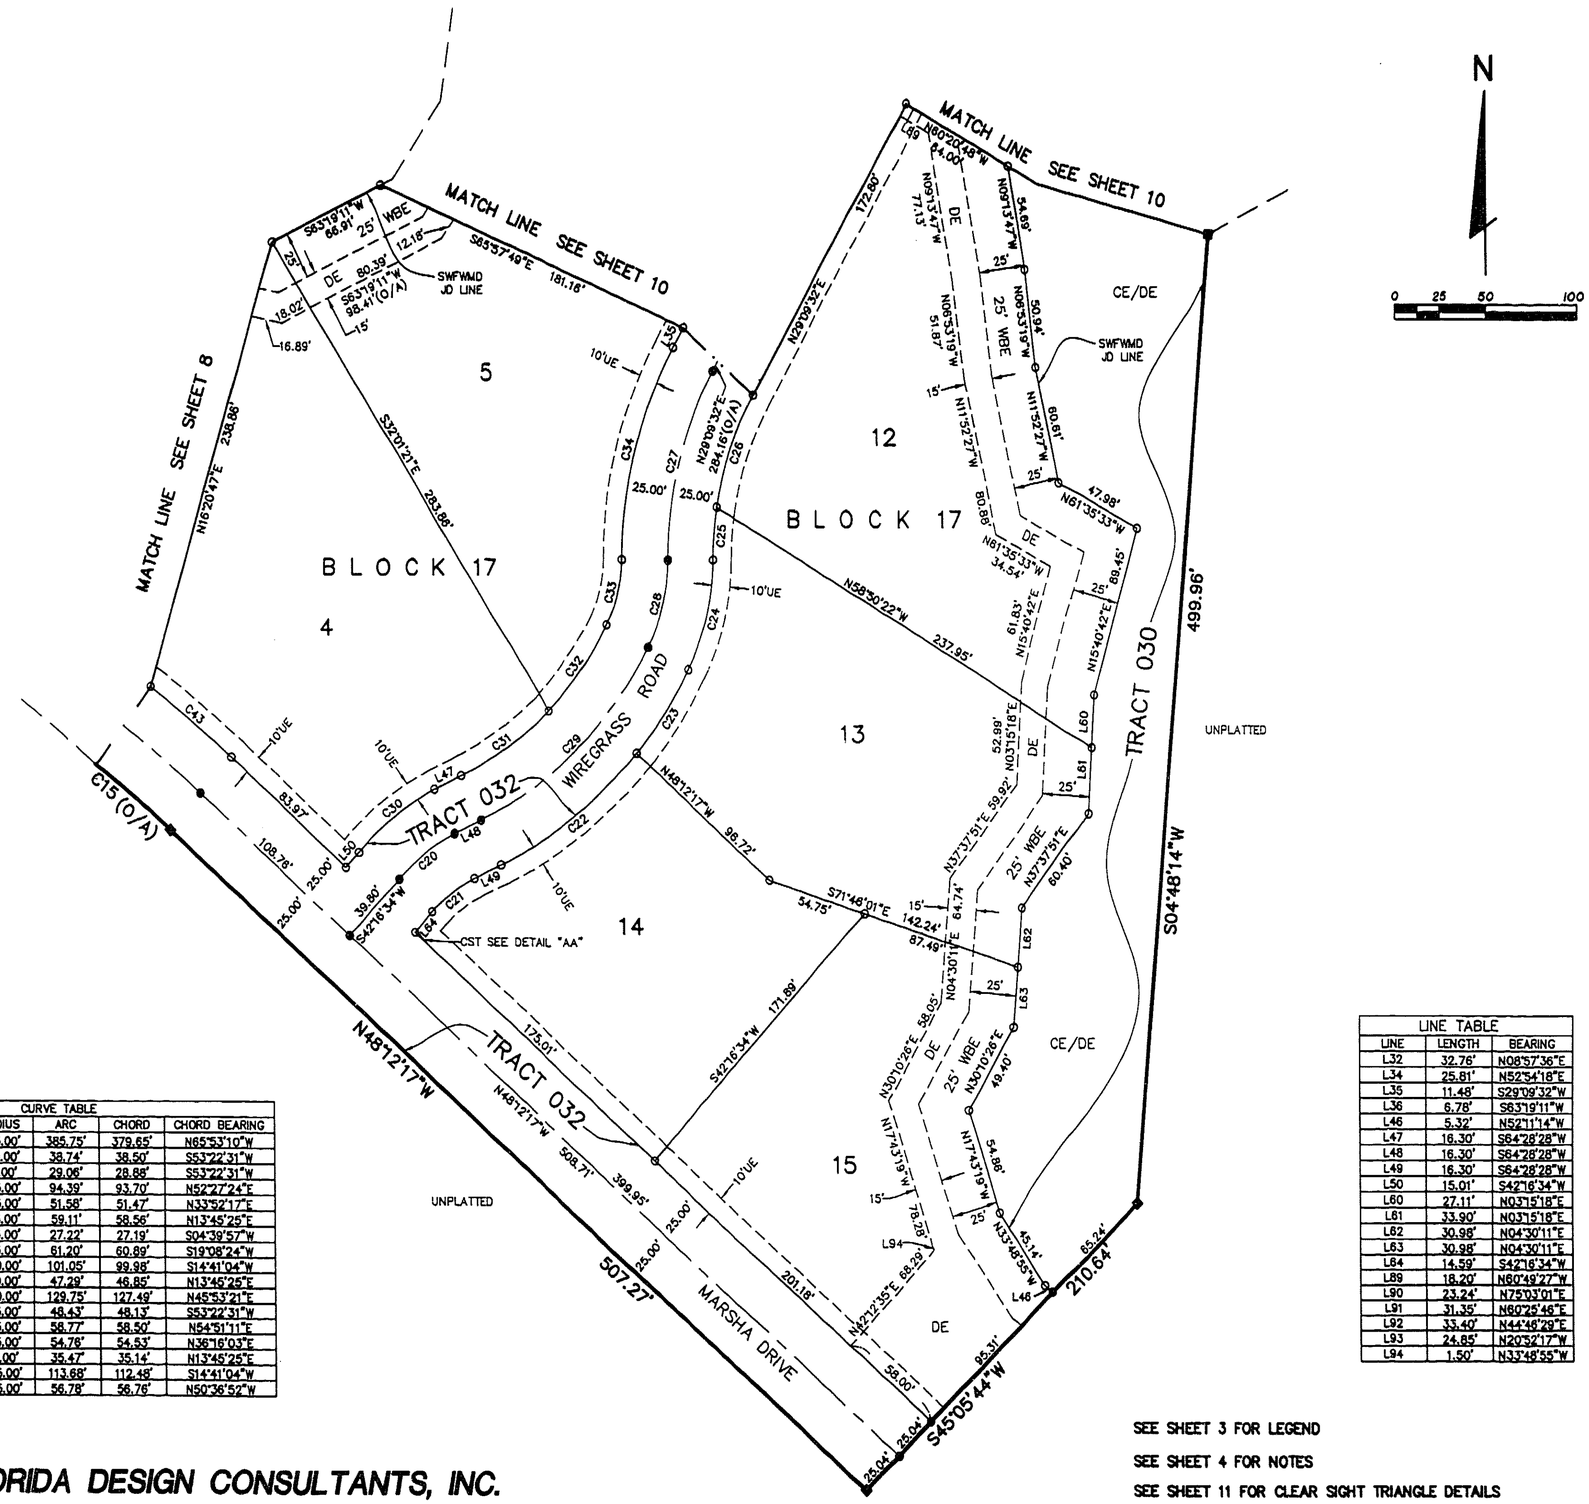

CURVE TABLE					
CURVE	DELTA	RADIUS	ARC	CHORD	CHORD BEARING
C15	35°21'45"	625.00'	385.75'	379.65'	N65°53'10"W
C20	22°11'54"	100.00'	38.74'	38.50'	S53°22'31"W
C21	22°11'54"	75.00'	29.06'	28.88'	S53°22'31"W
C22	24°02'08"	225.00'	94.39'	93.70'	N52°27'24"E
C23	13°08'07"	225.00'	51.58'	51.47'	N33°52'17"E
C24	27°05'36"	125.00'	59.11'	58.56'	N13°45'25"E
C25	8°54'40"	175.00'	27.22'	27.19'	S04°39'57"W
C26	20°02'14"	175.00'	61.20'	60.89'	S19°08'24"W
C27	28°56'55"	200.00'	101.05'	99.98'	S14°41'04"W
C28	27°05'36"	100.00'	47.29'	46.85'	N13°45'25"E
C29	37°10'15"	200.00'	129.75'	127.49'	N45°53'21"E
C30	22°11'54"	125.00'	48.43'	48.13'	S53°22'31"W
C31	19°14'34"	175.00'	58.77'	58.50'	N54°51'11"E
C32	17°55'40"	175.00'	54.76'	54.53'	N36°16'03"E
C33	27°05'36"	75.00'	35.47'	35.14'	N13°45'25"E
C34	28°56'55"	225.00'	113.68'	112.48'	S14°41'04"W
C43	4°49'11"	675.00'	56.78'	56.76'	N50°36'52"W

LINE TABLE		
LINE	LENGTH	BEARING
L32	32.76'	N08°57'36"E
L34	25.81'	N52°54'18"E
L35	11.48'	S29°09'32"W
L36	6.78'	S63°19'11"W
L46	5.32'	N52°11'14"W
L47	16.30'	S64°28'28"W
L48	16.30'	S64°28'28"W
L49	16.30'	S64°28'28"W
L50	15.01'	S42°16'34"W
L60	27.11'	N03°15'18"E
L61	33.90'	N03°15'18"E
L62	30.98'	N04°30'11"E
L63	30.98'	N04°30'11"E
L64	14.59'	S42°16'34"W
L89	18.20'	N60°49'27"W
L90	23.24'	N75°03'01"E
L91	31.35'	N60°25'46"E
L92	33.40'	N44°46'29"E
L93	24.85'	N20°52'17"W
L94	1.50'	N33°48'55"W

SEE SHEET 3 FOR LEGEND

SEE SHEET 4 FOR NOTES

SEE SHEET 11 FOR CLEAR SIGHT TRIANGLE DETAILS

FLORIDA DESIGN CONSULTANTS, INC.
ENGINEERS, ENVIRONMENTALISTS, SURVEYORS & PLANNERS
6321 Grand Boulevard, New Port Richey FL 34652
Tel: (727) 849-7588 - Fax: (727) 848-3648
Certificate of Authorization: LB 6707
State of Florida

NOTE:
This plat, as recorded in its graphic form, is the official depiction of the subdivided lands described herein and will in no circumstance be supplanted in authority by any other graphic or digital form of the plat.
There may be additional restrictions that are not recorded on this plat that may be found in the Public Records of this County.