LONGLEAF NEIGHBORHOOD TWO
PHASE ONE AND PHASE THREE

BEING A SUBDIVISION OF LAND LYING WITHIN SECTION 19, TOWNSHIP 26 SOUTH, RANGE 17 EAST, PASCO COUNTY, FLORIDA

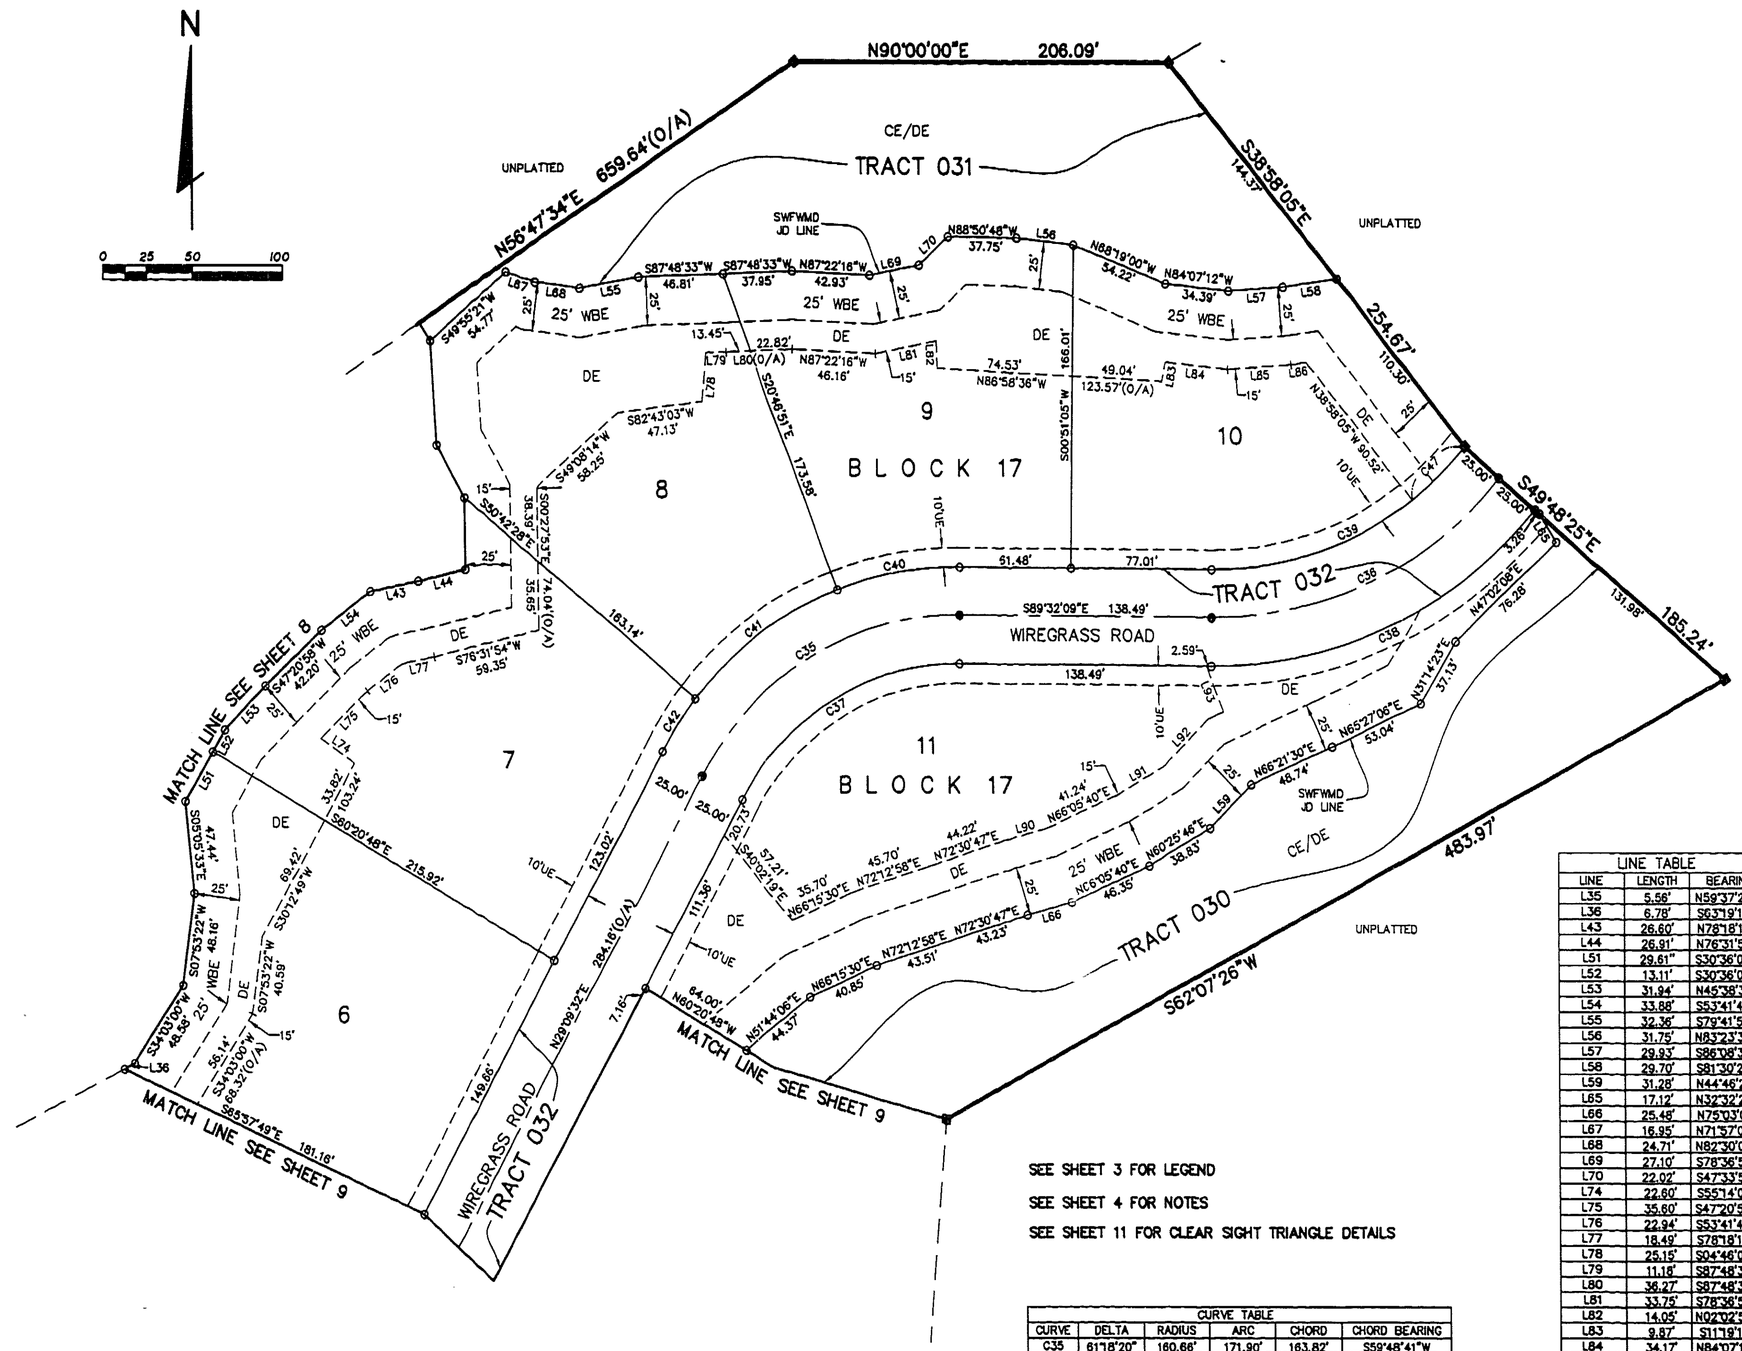

SEE SHEET 3 FOR LEGEND

SEE SHEET 4 FOR NOTES

SEE SHEET 11 FOR CLEAR SIGHT TRIANGLE DETAILS

CURVE TABLE					
CURVE	DELTA	RADIUS	ARC	CHORD	CHORD BEARING
C35	61°16'20"	160.66'	171.90'	163.82'	S59°48'41"W
C36	50°16'16"	204.63'	179.54'	173.83'	N65°19'43"E
C37	61°16'20"	135.66'	145.15'	138.33'	S59°48'41"W
C38	50°16'16"	229.63'	201.47'	195.07'	N65°19'43"E
C39	50°16'16"	179.63'	157.60'	152.60'	N65°19'43"E
C40	21°14'43"	185.66'	68.84'	68.45'	S79°50'30"W
C41	29°55'36"	185.66'	96.97'	95.88'	S54°15'21"W
C42	10°08'01"	185.66'	32.84'	32.79'	S34°13'32"W
C46	13°39'22"	179.63'	42.81'	42.71'	N47°01'16"E

LINE TABLE		
LINE	LENGTH	BEARING
L35	5.56'	N59°37'21"W
L36	6.78'	S63°19'11"W
L43	26.60'	N78°18'19"E
L44	26.91'	N76°31'54"E
L51	29.61'	S30°36'00"W
L52	13.11'	S30°36'00"W
L53	31.94'	N45°38'36"E
L54	33.88'	S53°41'48"W
L55	32.36'	S79°41'55"W
L56	31.75'	N83°23'37"W
L57	29.93'	S86°08'32"W
L58	29.70'	S81°30'29"W
L59	31.28'	N44°46'29"E
L65	17.12'	N32°32'21"W
L66	25.48'	N75°03'01"E
L67	16.95'	N71°57'05"W
L68	24.71'	N82°30'08"W
L69	27.10'	S78°36'53"W
L70	22.02'	S47°33'50"W
L74	22.60'	S55°14'04"E
L75	35.60'	S47°20'58"W
L76	22.94'	S53°41'48"W
L77	18.49'	S78°18'19"W
L78	25.15'	S04°46'04"W
L79	11.18'	S87°48'33"W
L80	36.27'	S87°48'33"W
L81	33.75'	S78°36'53"W
L82	14.05'	N02°02'50"W
L83	9.87'	S11°19'11"W
L84	34.17'	N84°07'12"W
L85	34.96'	S86°08'32"W
L86	11.59'	S81°30'29"W
L87	18.31'	N45°58'28"W
L90	23.24'	N75°03'01"E
L91	31.35'	N60°25'46"E
L92	33.40'	N44°46'29"E
L93	24.85'	N20°52'17"W
L94	1.50'	N33°48'55"W

FLORIDA DESIGN CONSULTANTS, INC.
ENGINEERS, ENVIRONMENTALISTS, SURVEYORS & PLANNERS
6321 Grand Boulevard, New Port Richey FL 34652
Tel. (727) 849-7568 - Fax. (727) 848-3648
Certificate of Authorization: LB 6707
State of Florida

NOTE:
This plat, as recorded in its graphic form, is the official depiction of the subdivided lands described herein and will in no circumstance be supplanted in authority by any other graphic or digital form of the plat.
There may be additional restrictions that are not recorded on this plat that may be found in the Public Records of this County.