ARISTIDA PHASE II - B

A SUBDIVISION OF A PORTION OF THE SOUTH 1/2 OF SECTION 7, TOWNSHIP 26 SOUTH, RANGE 17 EAST, PASCO COUNTY, FLORIDA.

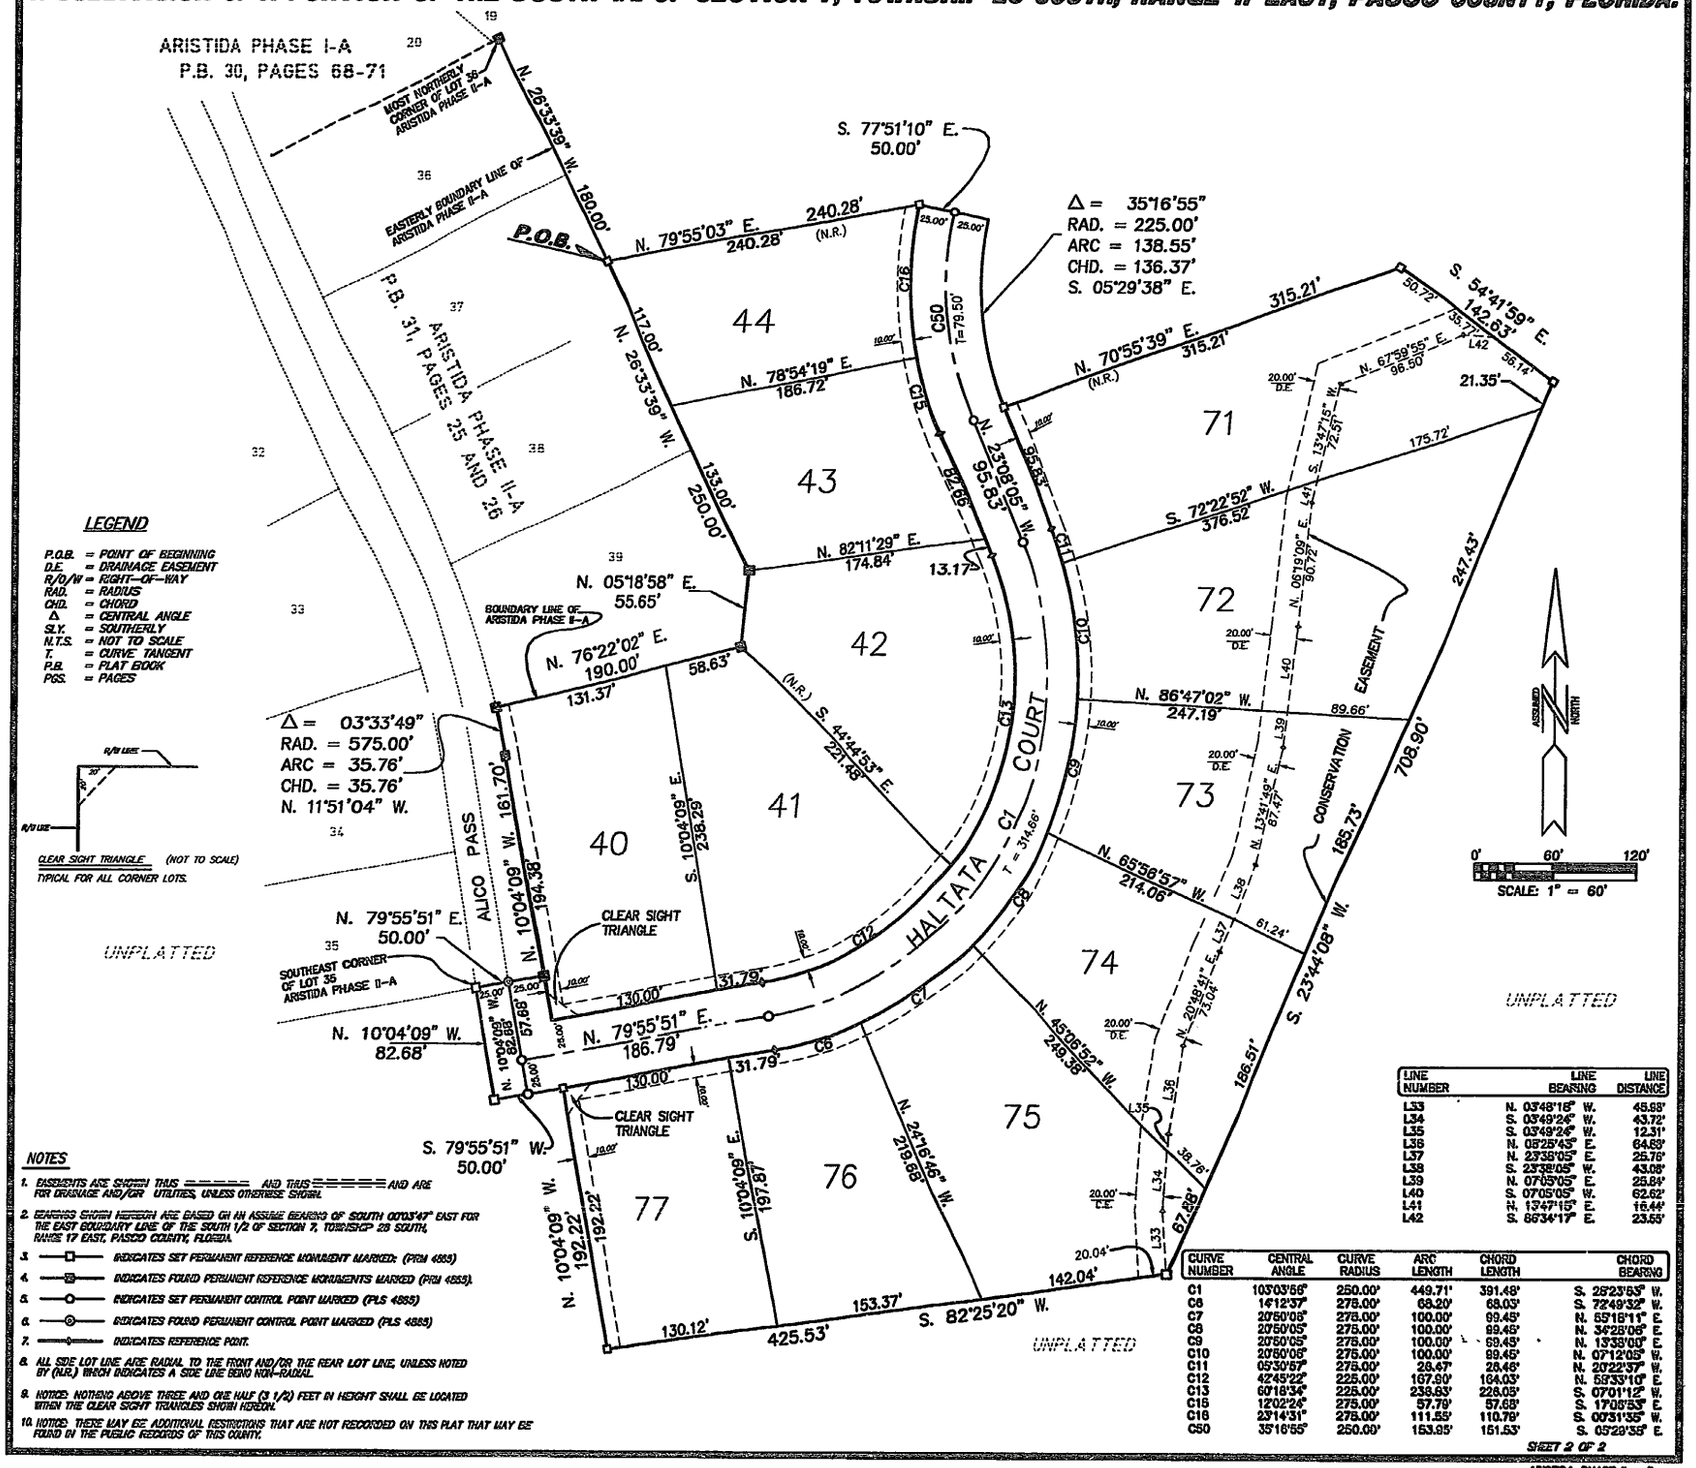

LEGEND

P.O.B. = POINT OF BEGINNING
D.E. = DRAINAGE EASEMENT
R/O/W = RIGHT-OF-WAY
RAD. = RADIUS
CHD. = CHORD
Δ = CENTRAL ANGLE
S.L.Y. = SOUTHERLY
N.T.S. = NOT TO SCALE
T. = CURVE TANGENT
P.B. = PLAT BOOK
PGS. = PAGES

CLEAR SIGHT TRIANGLE (NOT TO SCALE)
TYPICAL FOR ALL CORNER LOTS.

NOTES

1. EASEMENTS ARE SHOWN THUS ======= AND THUS ======= AND ARE FOR DRAINAGE AND/OR UTILITIES, UNLESS OTHERWISE SHOWN.
2. BEARINGS SHOWN HEREON ARE BASED ON AN ASSUME BEARING OF SOUTH 00°03'47" EAST FOR THE EAST BOUNDARY LINE OF THE SOUTH 1/2 OF SECTION 7, TOWNSHIP 26 SOUTH, RANGE 17 EAST, PASCO COUNTY, FLORIDA.
3. —□— INDICATES SET PERMANENT REFERENCE MONUMENT MARKED: (PRM 4885)
4. —■— INDICATES FOUND PERMANENT REFERENCE MONUMENTS MARKED (PRM 4885).
5. —○— INDICATES SET PERMANENT CONTROL POINT MARKED (PLS 4885)
6. —◎— INDICATES FOUND PERMANENT CONTROL POINT MARKED (PLS 4885)
7. —◇— INDICATES REFERENCE POINT.
8. ALL SIDE LOT LINE ARE RADIAL TO THE FRONT AND/OR THE REAR LOT LINE, UNLESS NOTED BY (N.R.) WHICH INDICATES A SIDE LINE BEING NON-RADIAL.
9. NOTICE: NOTHING ABOVE THREE AND ONE HALF (3 1/2) FEET IN HEIGHT SHALL BE LOCATED WITHIN THE CLEAR SIGHT TRIANGLES SHOWN HEREON.
10. NOTICE: THERE MAY BE ADDITIONAL RESTRICTIONS THAT ARE NOT RECORDED ON THIS PLAT THAT MAY BE FOUND IN THE PUBLIC RECORDS OF THIS COUNTY.

LINE NUMBER	LINE BEARING	LINE DISTANCE
L33	N. 03°48'16" W.	45.98'
L34	S. 03°49'24" W.	43.72'
L35	S. 03°49'24" W.	12.31'
L36	N. 05°25'43" E.	64.83'
L37	N. 23°38'05" E.	25.76'
L38	S. 23°38'05" W.	43.08'
L39	N. 07°05'05" E.	25.84'
L40	S. 07°05'05" W.	62.62'
L41	N. 13°47'15" E.	16.44'
L42	S. 86°34'17" E.	23.55'

CURVE NUMBER	CENTRAL ANGLE	CURVE RADIUS	ARC LENGTH	CHORD LENGTH	CHORD BEARING
C1	103°03'56"	250.00'	449.71'	391.48'	S. 28°23'53" W.
C6	14°12'37"	275.00'	68.20'	68.03'	S. 72°49'32" W.
C7	20°50'06"	275.00'	100.00'	99.45'	N. 65°16'11" E.
C8	20°50'05"	275.00'	100.00'	99.45'	N. 34°28'06" E.
C9	20°50'05"	275.00'	100.00'	99.45'	N. 13°33'00" E.
C10	20°50'06"	275.00'	100.00'	99.45'	N. 07°12'05" W.
C11	05°30'57"	275.00'	26.47'	26.46'	N. 20°22'37" W.
C12	42°45'22"	225.00'	167.90'	164.03'	N. 59°33'10" E.
C13	60°16'34"	225.00'	236.63'	226.05'	S. 07°01'12" W.
C15	12°02'24"	275.00'	57.79'	57.68'	S. 17°05'53" E.
C16	23°14'31"	275.00'	111.55'	110.79'	S. 00°31'35" W.
C50	35°16'55"	250.00'	153.95'	151.53'	S. 05°29'38" E.

SHEET 2 OF 2