LAKE CALOOSA LANDING , PHASE II

A PORTION OF SECTION 22 TOWNSHIP 31 SOUTH, RANGE 27 EAST, POLK COUNTY, FLORIDA

PLAT BOOK 89
PAGE 6

NOTE: BEARING DATUM BASED ON SOUTH LINE OF SECTION 22 AS SHOWN.

■ - PERMENENT REFERENCE MONUMENT

● - PERMENENT CONTROL POINT

SCALE - 1" = 200'

0' 100' 200' 400'

NORTH

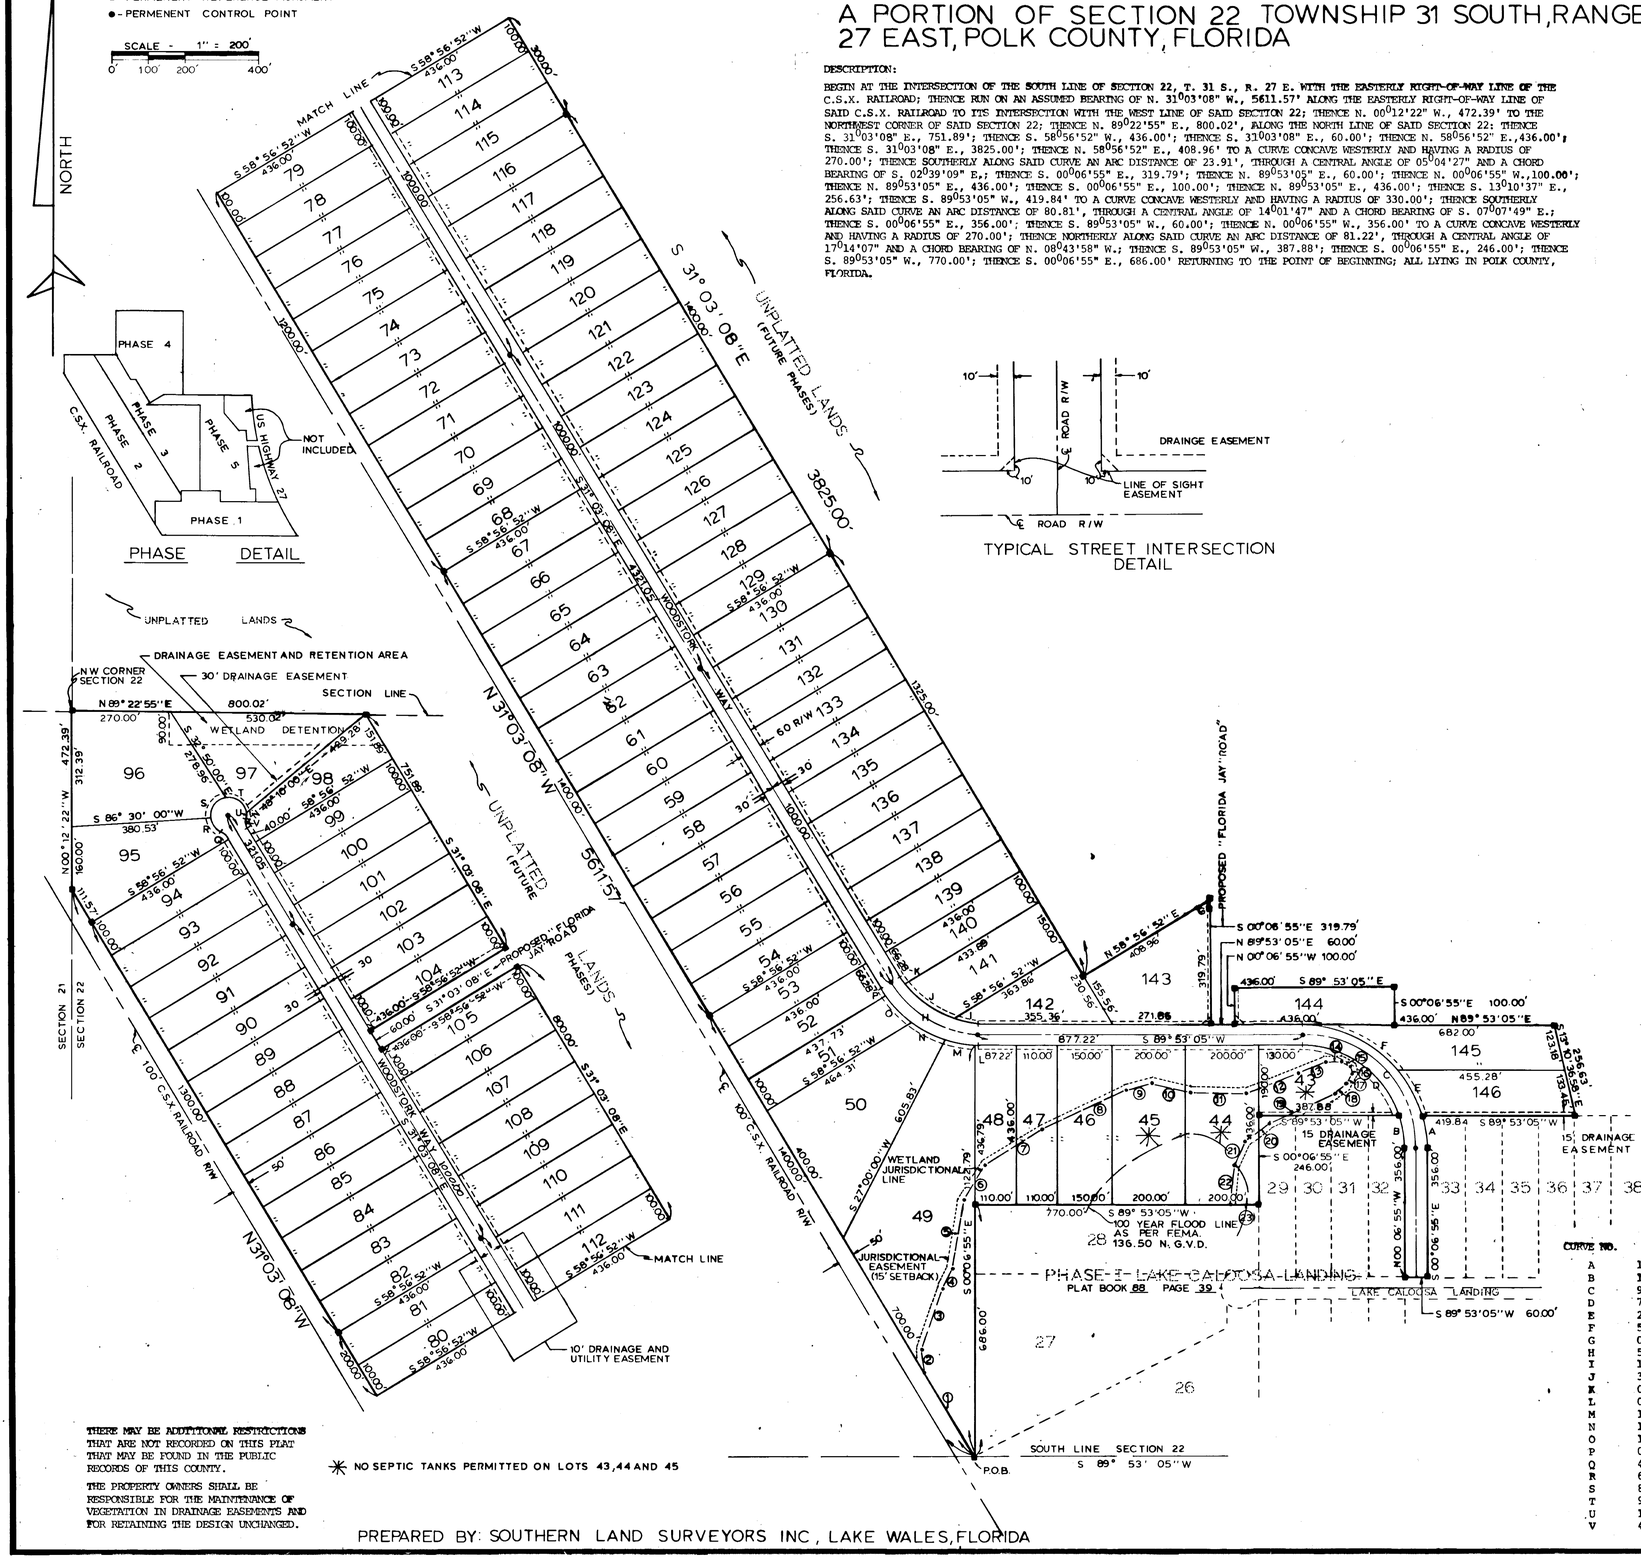

TYPICAL STREET INTERSECTION DETAIL

DESCRIPTION:

BEGIN AT THE INTERSECTION OF THE SOUTH LINE OF SECTION 22, T. 31 S., R. 27 E. WITH THE EASTERLY RIGHT-OF-WAY LINE OF THE C.S.X. RAILROAD; THENCE RUN ON AN ASSUMED BEARING OF N. 31°03'08" W., 5611.57' ALONG THE EASTERLY RIGHT-OF-WAY LINE OF SAID C.S.X. RAILROAD TO ITS INTERSECTION WITH THE WEST LINE OF SAID SECTION 22; THENCE N. 00°12'22" W., 472.39' TO THE NORTHWEST CORNER OF SAID SECTION 22; THENCE N. 89°22'55" E., 800.02', ALONG THE NORTH LINE OF SAID SECTION 22: THENCE S. 31°03'08" E., 751.89'; THENCE S. 58°56'52" W., 436.00'; THENCE S. 31°03'08" E., 60.00'; THENCE N. 58°56'52" E.,436.00'; THENCE S. 31°03'08" E., 3825.00'; THENCE N. 58°56'52" E., 408.96' TO A CURVE CONCAVE WESTERLY AND HAVING A RADIUS OF 270.00'; THENCE SOUTHERLY ALONG SAID CURVE AN ARC DISTANCE OF 23.91', THROUGH A CENTRAL ANGLE OF 05°04'27" AND A CHORD BEARING OF S. 02°39'09" E.; THENCE S. 00°06'55" E., 319.79'; THENCE N. 89°53'05" E., 60.00'; THENCE N. 00°06'55" W.,100.00'; THENCE N. 89°53'05" E., 436.00'; THENCE S. 00°06'55" E., 100.00'; THENCE N. 89°53'05" E., 436.00'; THENCE S. 13°10'37" E., 256.63'; THENCE S. 89°53'05" W., 419.84' TO A CURVE CONCAVE WESTERLY AND HAVING A RADIUS OF 330.00'; THENCE SOUTHERLY ALONG SAID CURVE AN ARC DISTANCE OF 80.81', THROUGH A CENTRAL ANGLE OF 14°01'47" AND A CHORD BEARING OF S. 07°07'49" E.; THENCE S. 00°06'55" E., 356.00'; THENCE S. 89°53'05" W., 60.00'; THENCE N. 00°06'55" W., 356.00' TO A CURVE CONCAVE WESTERLY AND HAVING A RADIUS OF 270.00'; THENCE NORTHERLY ALONG SAID CURVE AN ARC DISTANCE OF 81.22', THROUGH A CENTRAL ANGLE OF 17°14'07" AND A CHORD BEARING OF N. 08°43'58" W.; THENCE S. 89°53'05" W., 387.88'; THENCE S. 00°06'55" E., 246.00'; THENCE S. 89°53'05" W., 770.00'; THENCE S. 00°06'55" E., 686.00' RETURNING TO THE POINT OF BEGINNING; ALL LYING IN POLK COUNTY, FLORIDA.

DEDICATION
STATE OF FLORIDA
COUNTY OF POLK

KNOW ALL MEN BY THESE PRESENTS THAT BOUNTIFUL LANDS, INC., A FLORIDA CORPORATION, OWNER OF THE HEREON DESCRIBED LANDS, HAS CAUSED THIS PLAT OF LAKE CALOOSA LANDING, PHASE 2 TO BE MADE AND DOES HEREBY DEDICATE TO THE PERPETUAL USE OF THE PUBLIC, ALL STREETS, DRIVES, RIGHT-OF-WAYS, AND/OR EASEMENTS FOR THE USE OR USES HEREON DESCRIBED: IN WITNESS WHEREOF IT HAS HEREUNTO SET ITS HAND AND SEAL THIS 23 DAY OF JANUARY, 1990, A.D.

R. C. Johnson
WITNESS
Christina M. Olentier
WITNESS

BOUNTIFUL LANDS, INC.
BY:
JOHN P. FAZZINI, PRESIDENT

ACKNOWLEDGEMENT
STATE OF FLORIDA
COUNTY OF POLK

I HEREBY CERTIFY THAT ON THIS DAY BEFORE ME PERSONALLY APPEARED JOHN P FAZZINI, PRESIDENT OF BOUNTIFUL LANDS, INC., TO ME WELL KNOWN TO BE THE PERSON DESCRIBED IN AND WHO EXECUTED THE FOREGOING DEDICATION AND HE ACKNOWLEDGED BEFORE ME THE EXECUTION THEREOF ON BEHALF OF THE CORPORATION.

WITNESS MY HAND AND OFFICIAL SEAL THIS 23 DAY OF January, 1990, A.D.

Joy Dotsenmier
NOTARY PUBLIC 10-31-92

APPROVAL: COUNTY ENGINEER
STATE OF FLORIDA
COUNTY OF POLK

THIS PLAT IS HEREBY APPROVED BY THE POLK COUNTY ENGINEERING DEPARTMENT THIS 16TH DAY OF FEBRUARY, 1990, A.D.

John S. Hovik
ASST COUNTY ENGINEER

APPROVAL: COUNTY COMMISSION
STATE OF FLORIDA
COUNTY OF POLK

THIS PLAT APPROVED THIS 30TH DAY OF January, 1990, A.D., BY THE BOARD OF COUNTY COMMISSIONERS OF POLK COUNTY, FLORIDA.

BOARD OF COUNTY COMMISSIONERS
BY: Ernie Lindsey
CHAIRMAN

ATTEST: E.D. "Bud" Dixon
CLERK

APPROVAL: PLANNING DEPARTMENT
STATE OF FLORIDA
COUNTY OF POLK

THIS PLAT IS HEREBY APPROVED BY THE POLK COUNTY PLANNING DEPARTMENT THIS 15TH DAY OF FEBRUARY, 1990, A.D.

DIRECTOR ROBERT D. ANDERS

CLERK OF CIRCUIT COURT
STATE OF FLORIDA
COUNTY OF POLK

I, E.D. "BUD" DIXON, CLERK OF CIRCUIT COURT OF POLK COUNTY, FLORIDA, DO HEREBY CERTIFY THAT THIS PLAT HAS BEEN ACCEPTED FOR RECORDING THIS 16TH DAY OF February, 1990, A.D.

E.D. "Bud" Dixon
CLERK OF CIRCUIT COURT

SURVEYOR'S CERTIFICATE
STATE OF FLORIDA
COUNTY OF POLK

I HEREBY CERTIFY THAT THIS PLAT IS A TRUE AND CORRECT REPRESENTATION OF THE HEREON DESCRIBED LAND WHICH WAS RECENTLY SURVEYED AND PLATTED UNDER MY DIRECTION AND SUPERVISION, AND THAT PERMANENT REFERENCE MONUMENTS AND PERMANENT CONTROL POINTS HAVE BEEN SET IN ACCORDANCE WITH THE PROVISIONS OF SECTION 177.091, FLORIDA STATUTES, AND SURVEY DATA COMPLIES WITH ALL THE REQUIREMENTS OF CHAPTER 177, FLORIDA STATUTES AND MEETS THE MINIMUM TECHNICAL STANDARDS AS ESTABLISHED BY THE FLORIDA BOARD OF LAND SURVEYORS. PURSUANT TO CHAPTER 472.027, FLORIDA STATUTES.

R. C. Johnson DECEMBER 15, 1989
ROY C. JOHNSON
FLORIDA REGISTERED LAND SURVEYOR,
NO. 3381

CURVE TABLE

CURVE NO.	DELTA	RADIUS	CHORD	ARC LENGTH	CHORD BEARING	TANGENT
A	14°01'47"	330.00'	80.60'	80.81'	S 07°07'49" E	
B	17°14'07"	270.00'	80.91'	81.22'		
C	90°00'00"	300.00'	424.26'	471.24'	N. 45°06'55" W.	300.00'
D	72°45'53"	270.00'	320.31'	342.90'		
E	25°29'30"	330.00'	145.61'	146.82'		
F	56°28'44"	330.00'	281.43'	290.74'		
G	05°04'27"	270.00'	23.90'	23.91'	S 02°39'09" E	
H	59°03'47"	300.00'	295.74'	309.25'	N. 60°35'01" W.	169.95'
I	16°11'04"	270.00'	76.01'	76.27'		
J	35°42'15"	270.00'	165.54'	168.25'		
K	07°10'28"	270.00'	33.79'	33.81'		
L	03°57'30"	330.00'	22.79'	22.80'		
M	14°52'21"	330.00'	85.42'	85.66'		
N	16°19'44"	330.00'	93.73'	94.05'		
O	18°02'22"	330.00'	103.47'	103.90'		
P	05°51'50"	330.00'	33.76'	33.77'		
Q	40°07'09"	35.00'	24.01'	24.51'		
R	61°24'10"	50.00'	51.06'	53.58'		
S	89°25'18"	50.00'	70.35'	78.04'		
T	96°55'04"	50.00'	74.85'	84.58'		
U	12°29'46"	50.00'	10.88'	10.90'		
V	40°07'09"	35.00'	24.01'	24.51'		

LINE TABLE

LINE NO.	BEARING	DISTANCE
1	N. 30°49'06" W.	266.05'
2	N. 06°00'00" W.	60.00'
3	N. 18°00'00" E.	180.00'
4	N. 25°00'00" E.	60.00'
5	N. 10°30'00" E.	190.00'
6	N. 37°00'00" E.	110.00'
7	N. 56°00'00" E.	185.00'
8	N. 65°00'00" E.	250.00'
9	N. 70°12'06" E.	65.66'
10	S. 80°00'00" E.	115.00'
11	EAST	150.00'
12	N. 71°00'00" E.	140.00'
13	N. 65°30'00" E.	80.00'
14	S. 89°00'00" E.	45.00'
15	S. 61°00'00" E.	25.00'
16	S. 15°30'00" E.	20.00'
17	S. 25°00'00" W.	30.00'
18	S. 51°00'00" W.	40.00'
19	S. 66°30'00" W.	200.00'
20	S. 51°30'00" W.	80.00'
21	S. 26°00'00" W.	70.00'
22	S. 07°00'00" W.	114.98'
23	S. 89°53'05" W.	81.53'

THERE MAY BE ADDITIONAL RESTRICTIONS THAT ARE NOT RECORDED ON THIS PLAT THAT MAY BE FOUND IN THE PUBLIC RECORDS OF THIS COUNTY.

THE PROPERTY OWNERS SHALL BE RESPONSIBLE FOR THE MAINTENANCE OF VEGETATION IN DRAINAGE EASEMENTS AND FOR RETAINING THE DESIGN UNCHANGED.

✳ NO SEPTIC TANKS PERMITTED ON LOTS 43,44 AND 45

PREPARED BY: SOUTHERN LAND SURVEYORS INC, LAKE WALES, FLORIDA